

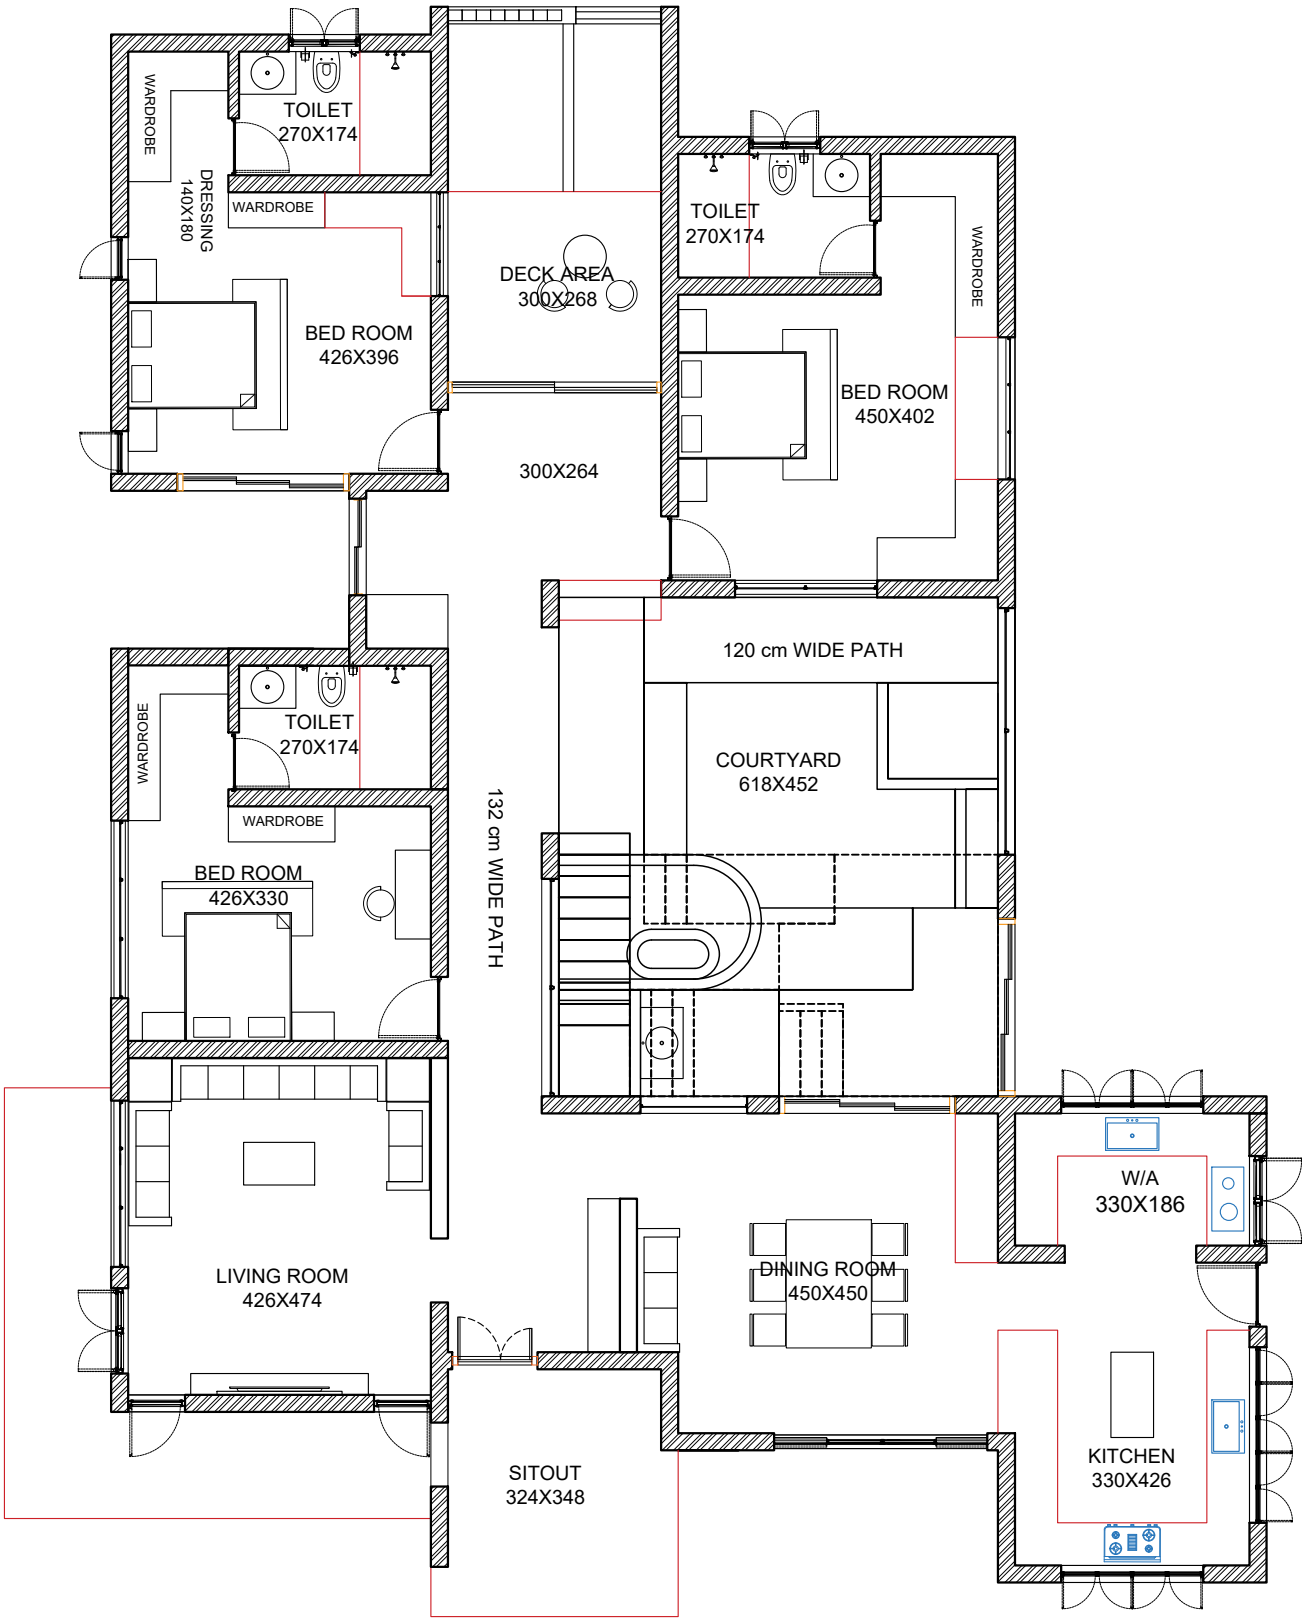


01 FURNITURE PLAN GROUND FLOOR


SCALE 1:100

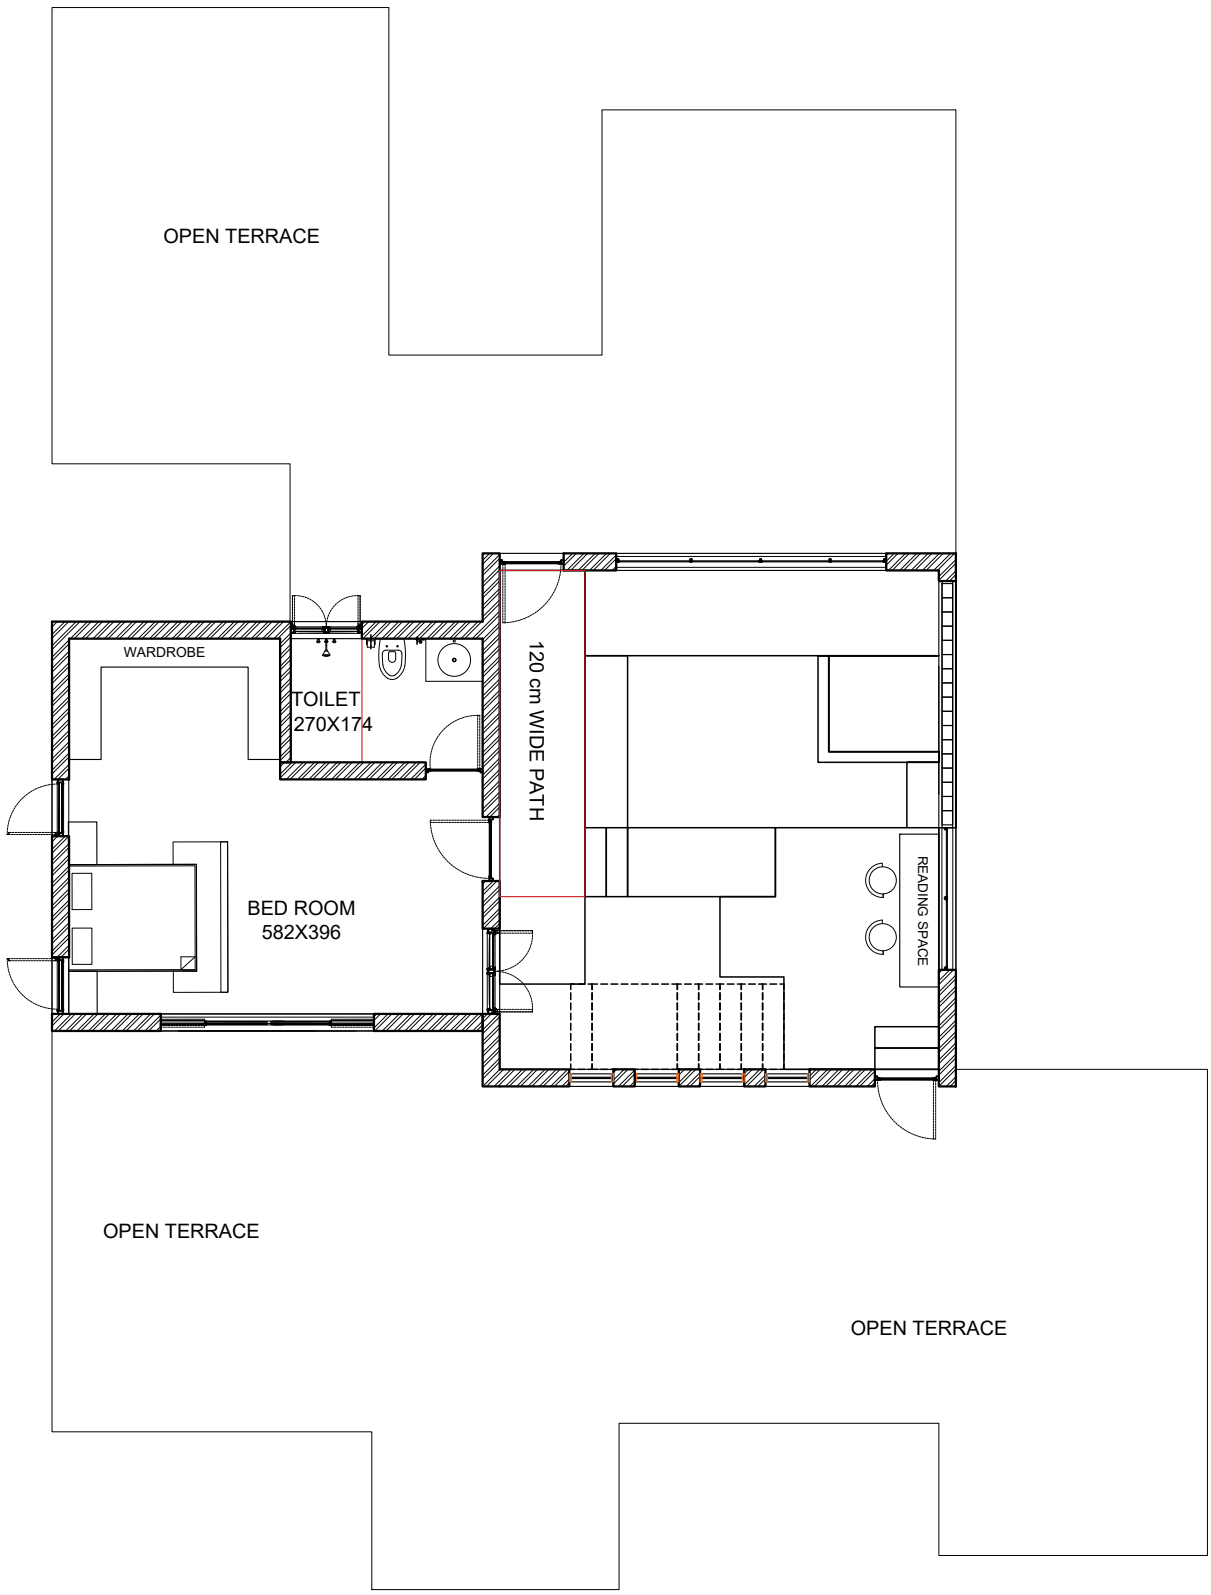

01 **FURNITURE PLAN**
FIRST FLOOR
SCALE 1:100

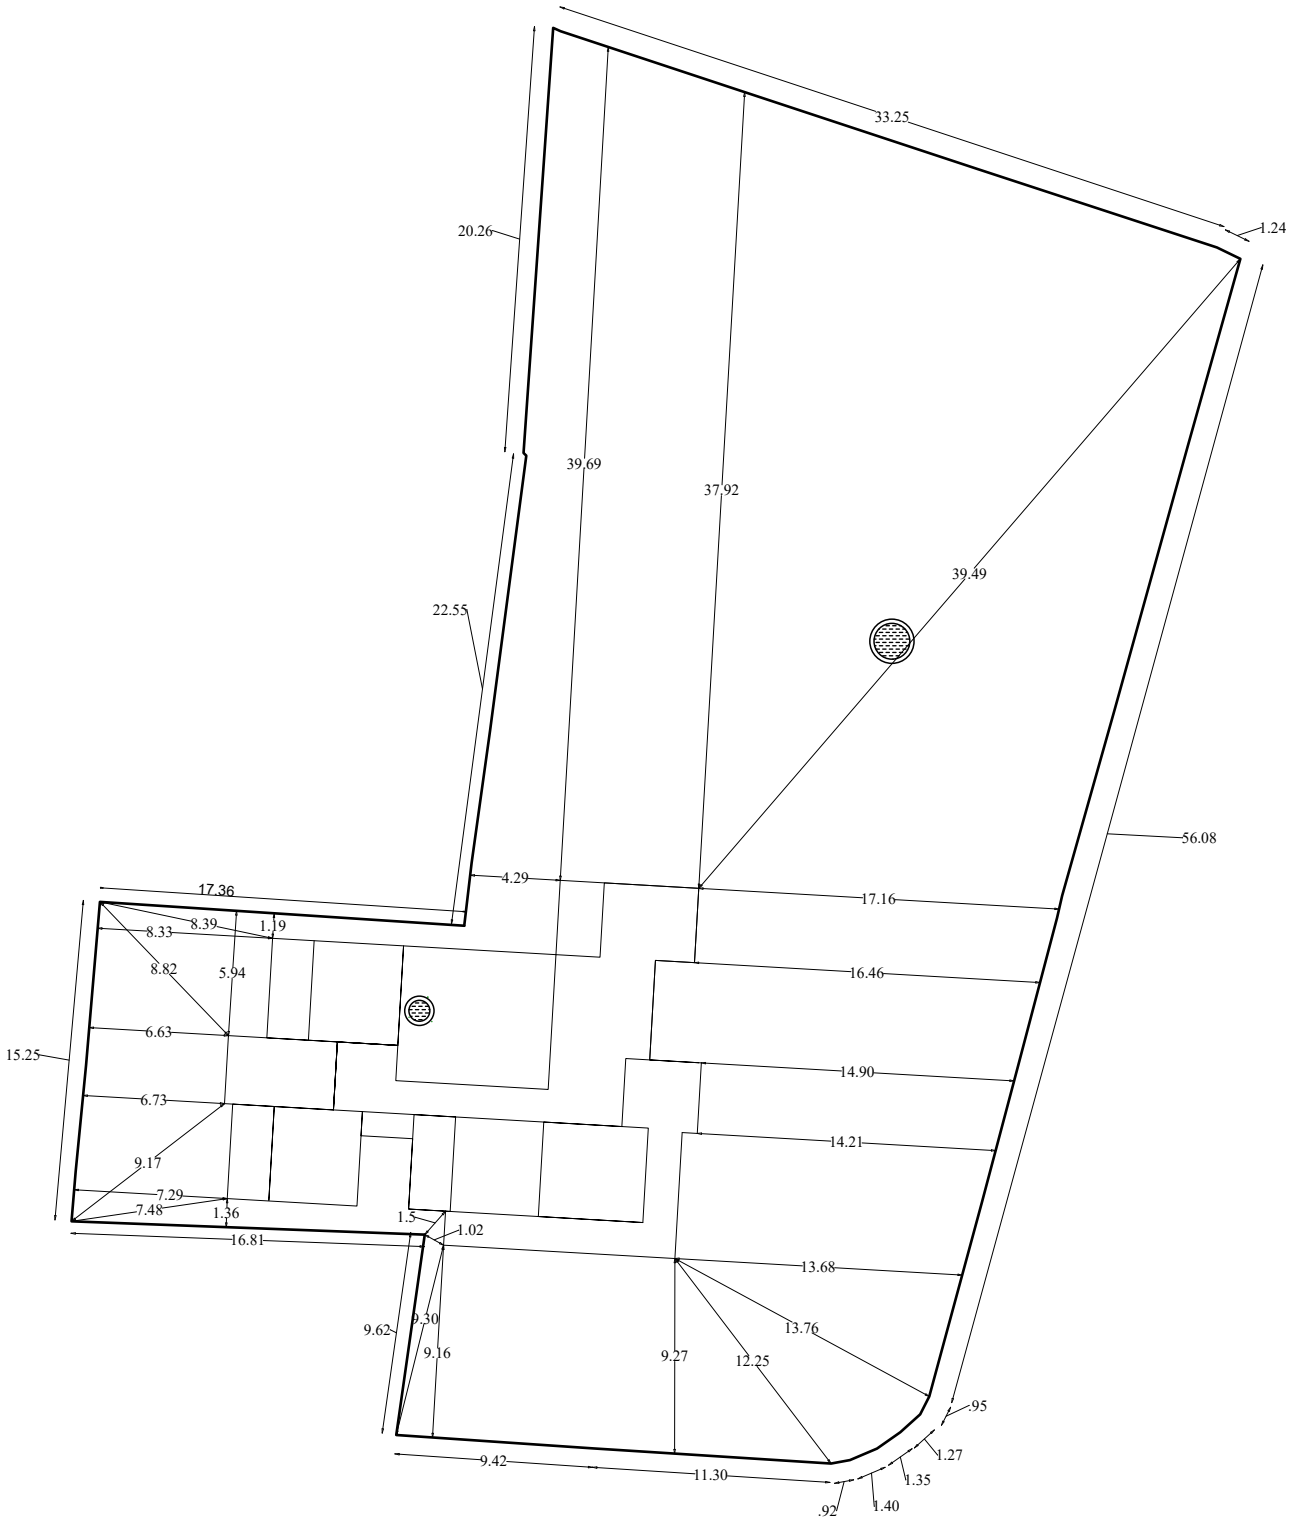



02 SETOUT
SCALE 1:100

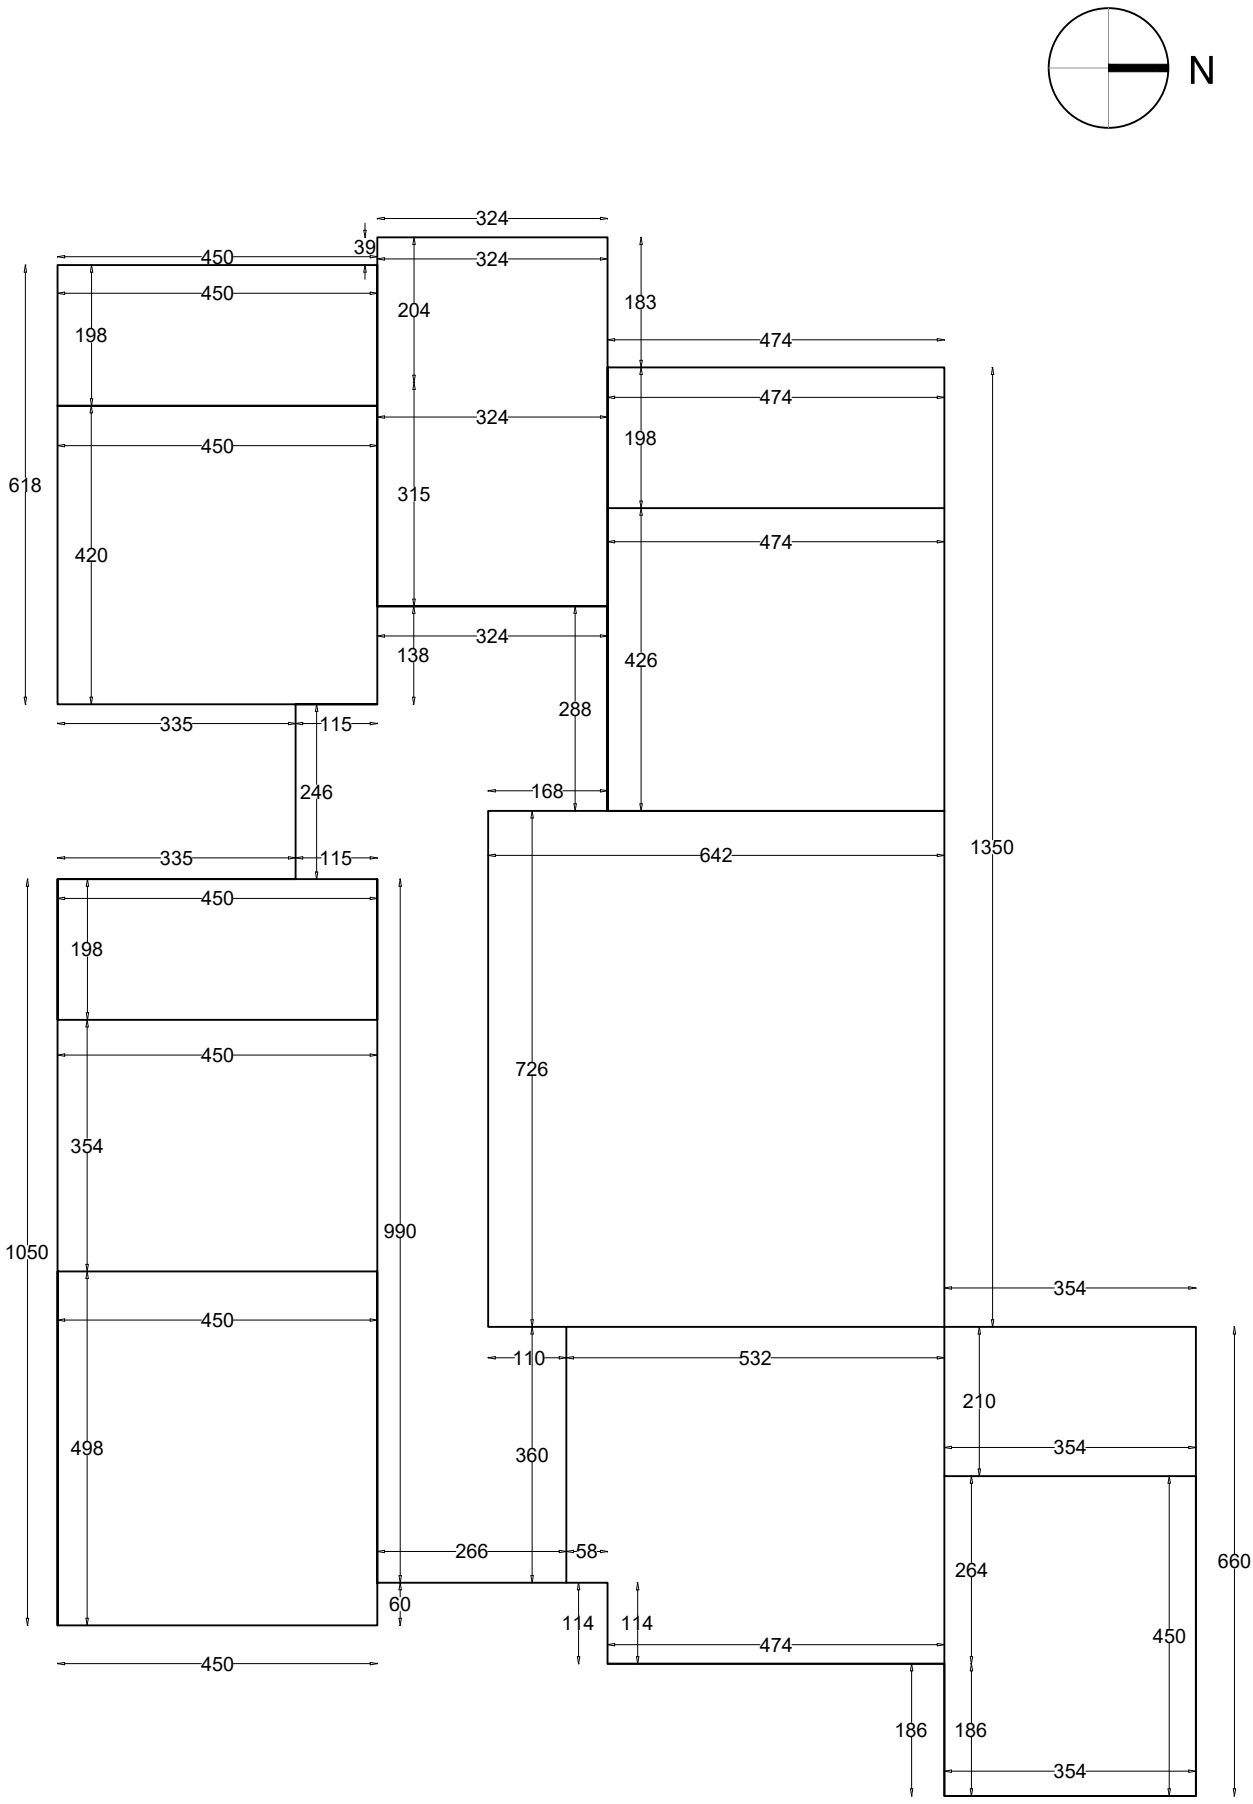

03 CENTRELINE WITH DIMENSION


SCALE 1:100

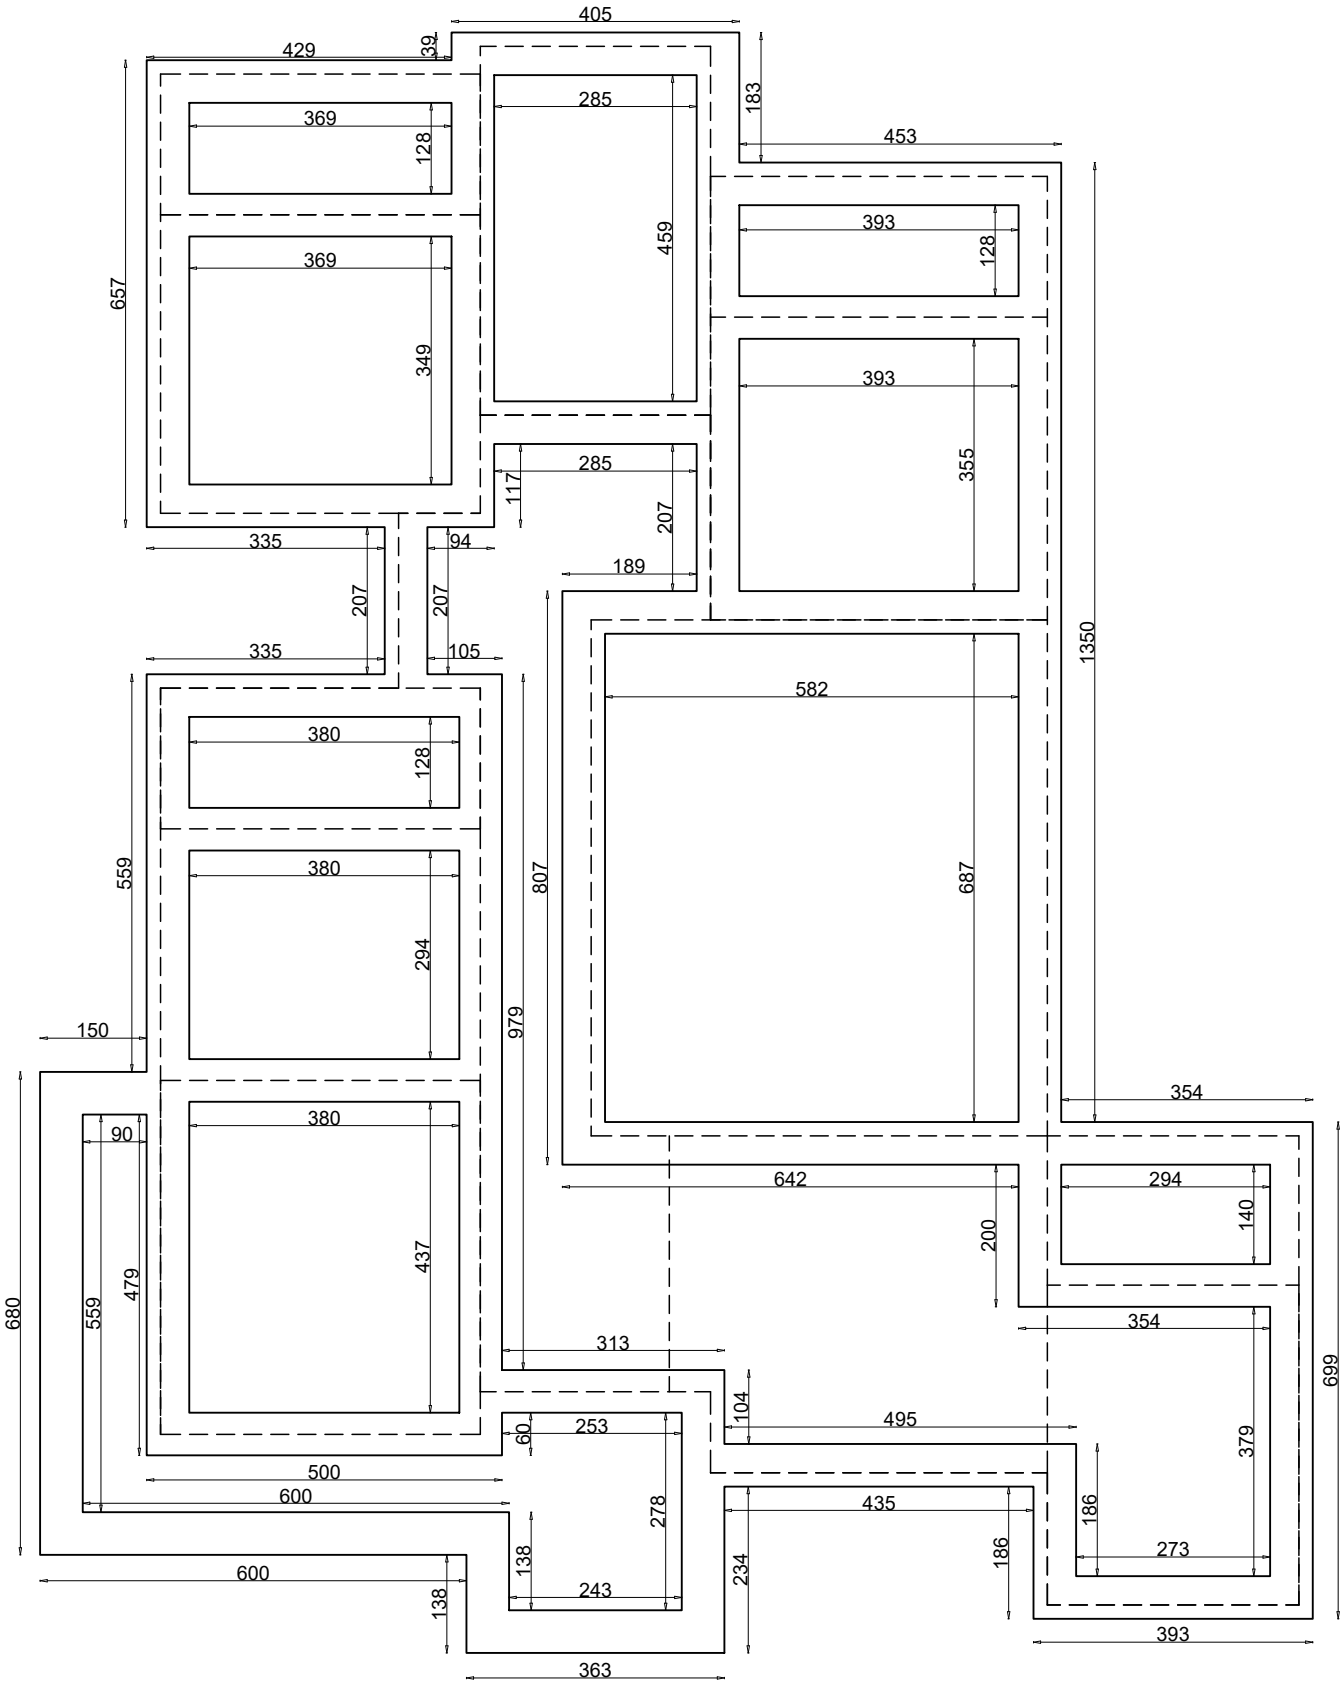
N
405
429
39
183
453
285
369
128
459
393
128
369
657
349
393
355
285
117
207
335
94
189
207
207
335
105
1350
582
380
128
687
559
380
807
294
150
979
380
354
90
642
294
140
437
200
680
559
479
354
313
699
104
495
379
60
253
500
600
278
435
186
186
273
138
243
234
600
138
393
363
FOUNDATION
DRAWING
04
SCALE 1:100

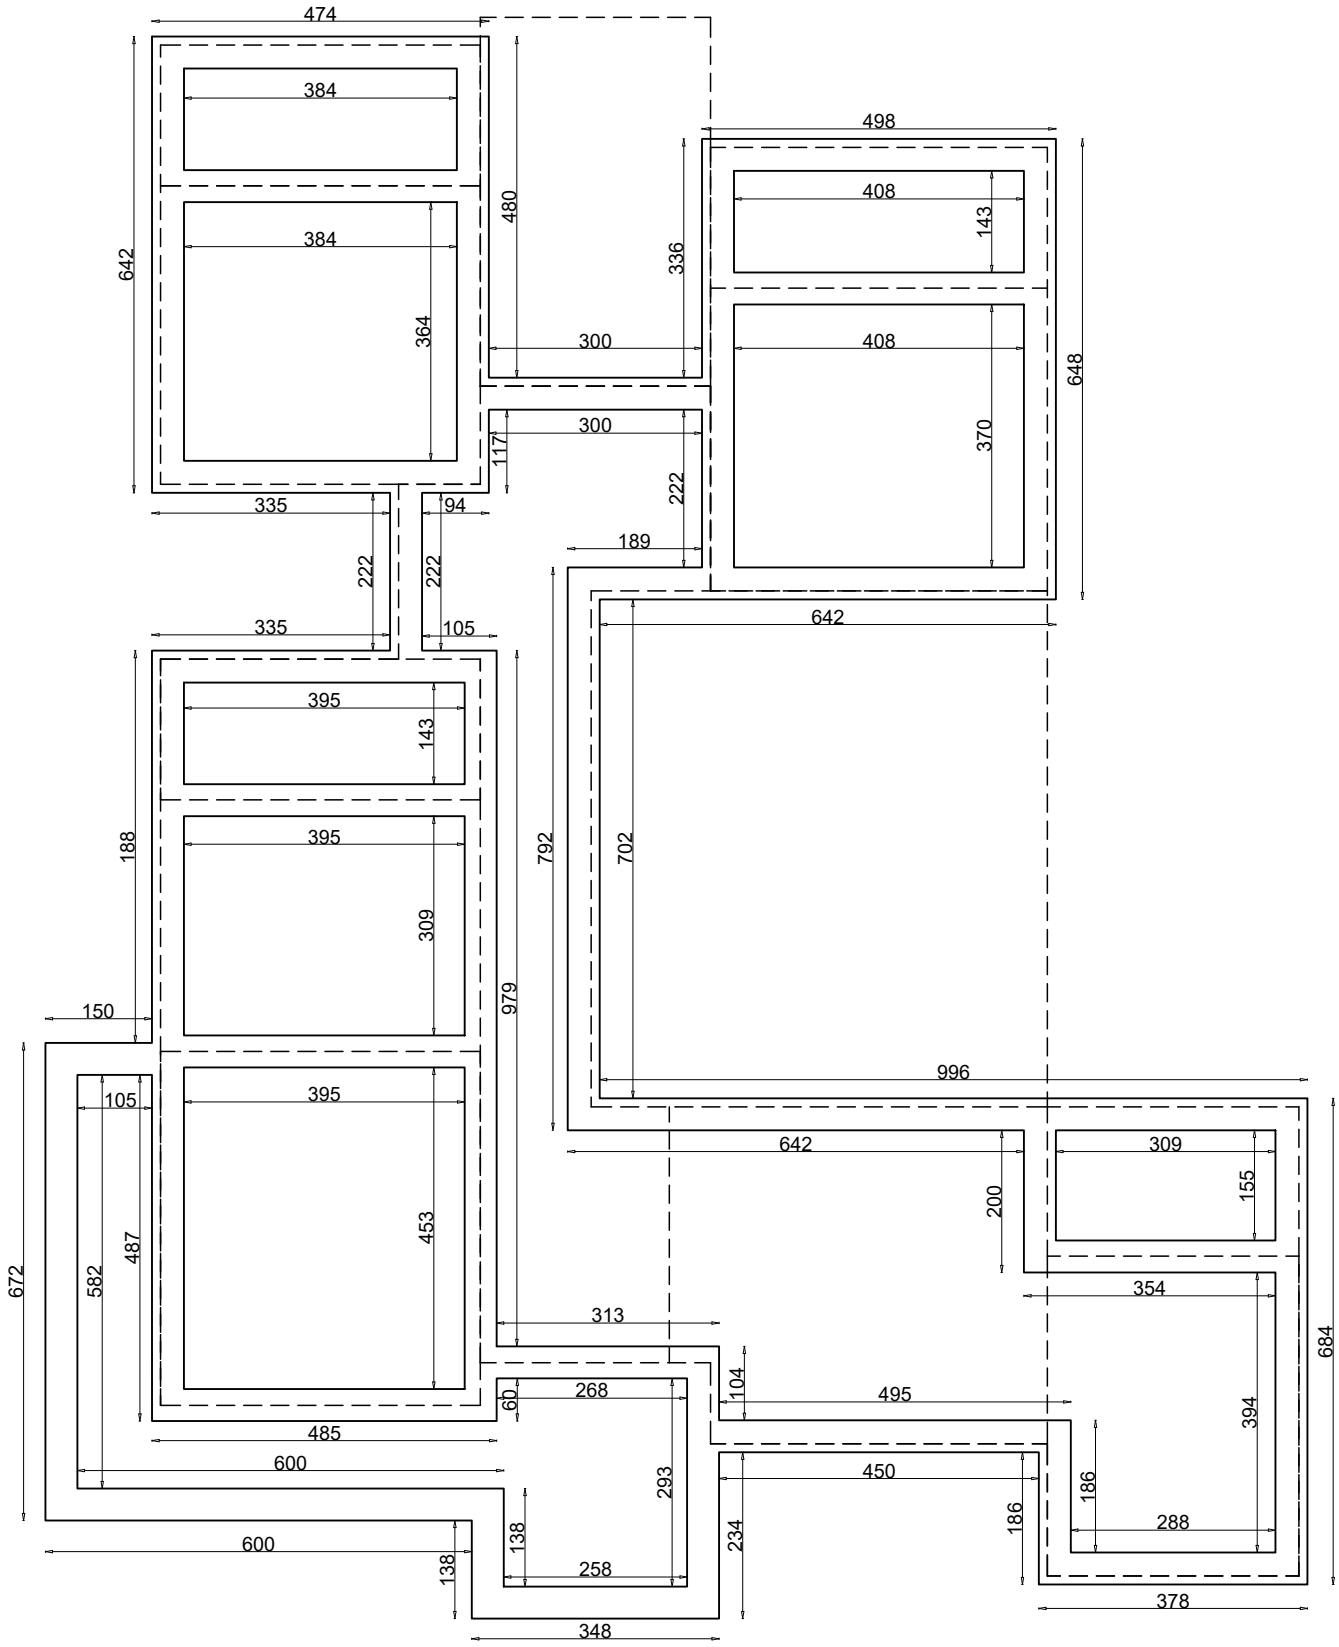


05 BASEMENT DRAWING

SCALE 1:100

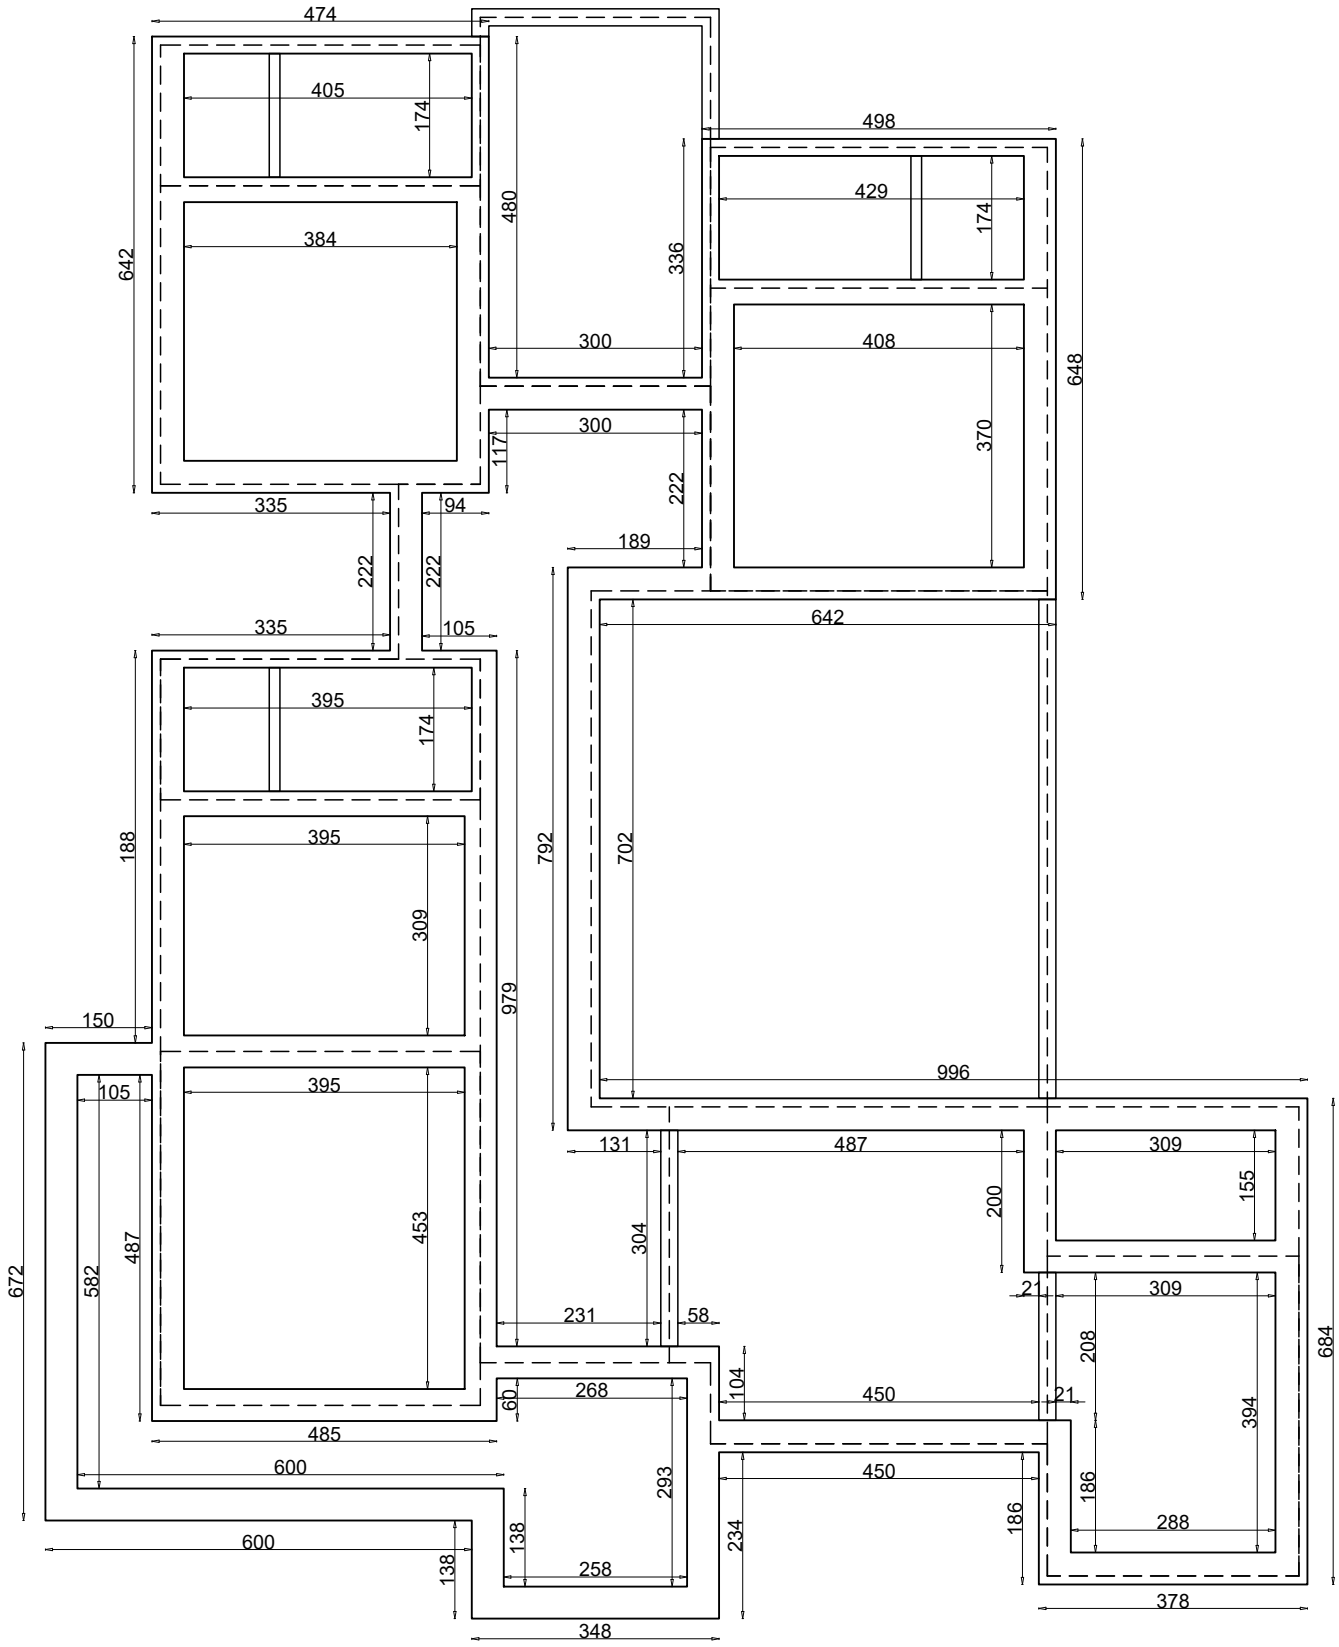


06 BELT DRAWING


SCALE 1:100

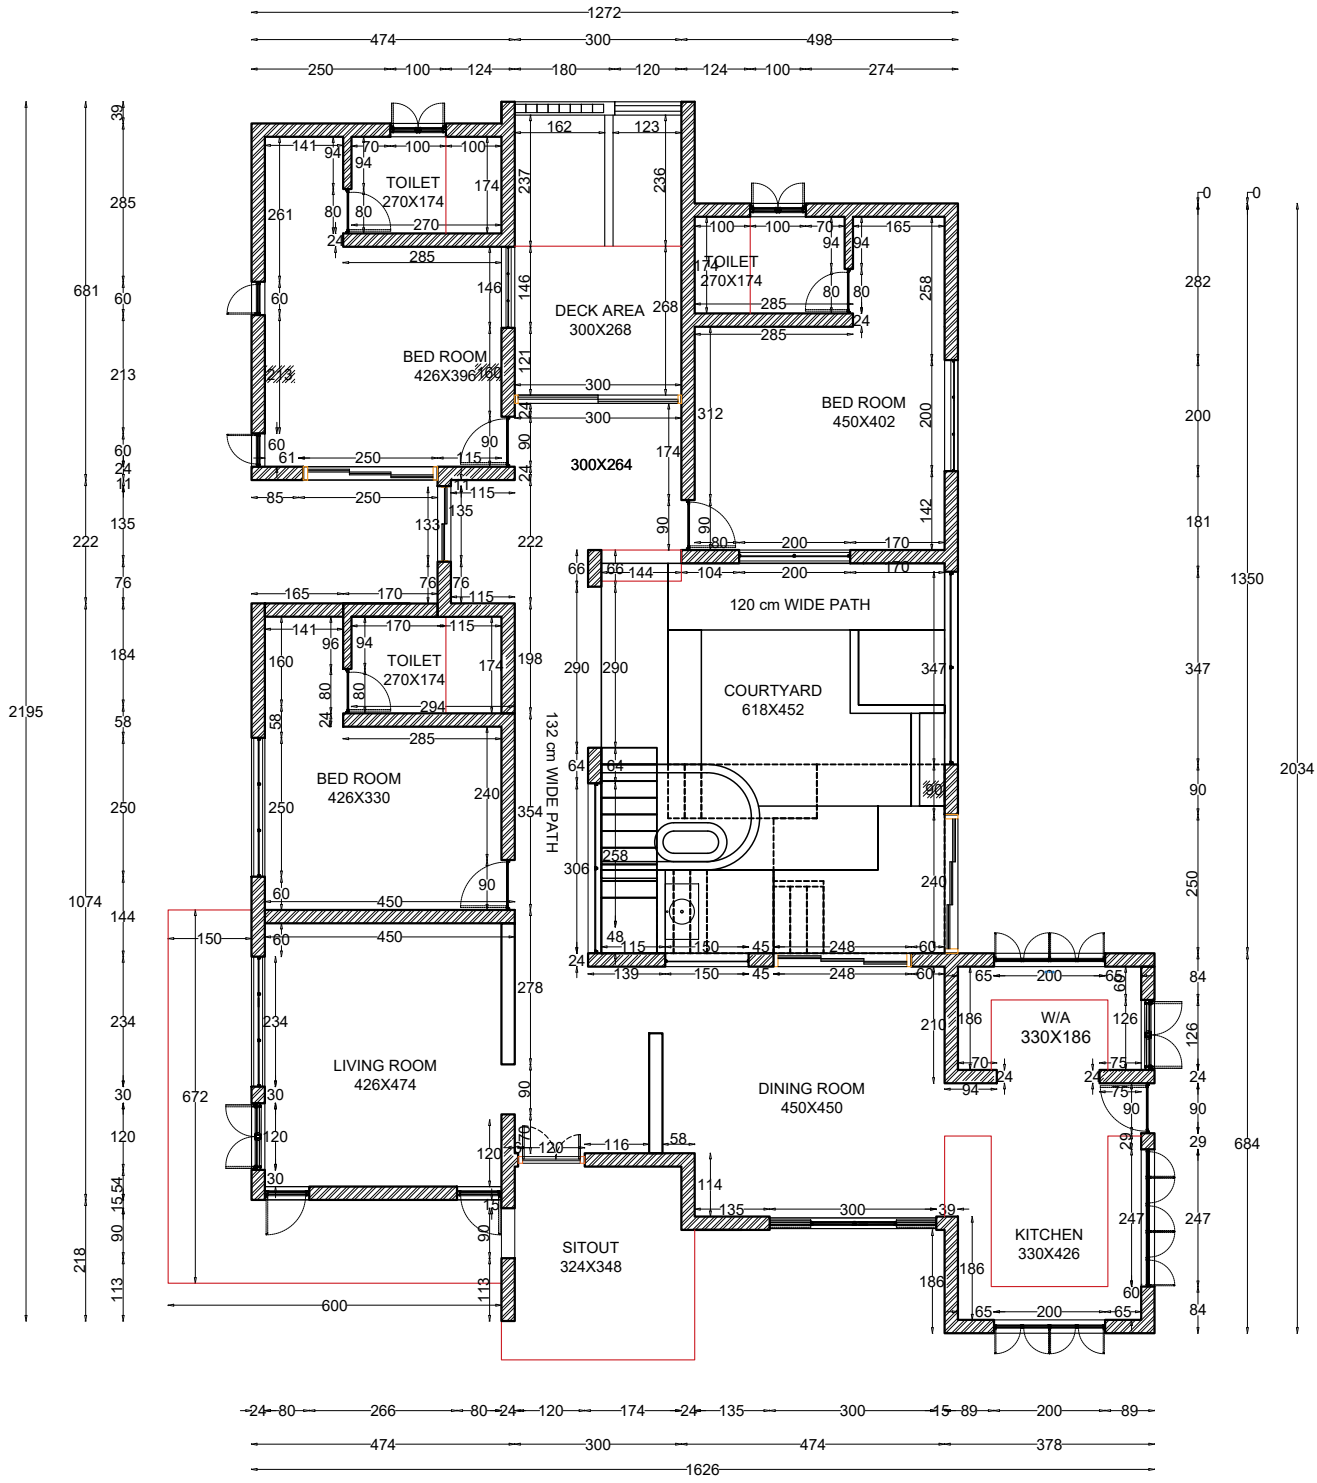

07 **MEASUREMENT**
GROUND FLOOR
SCALE 1:100

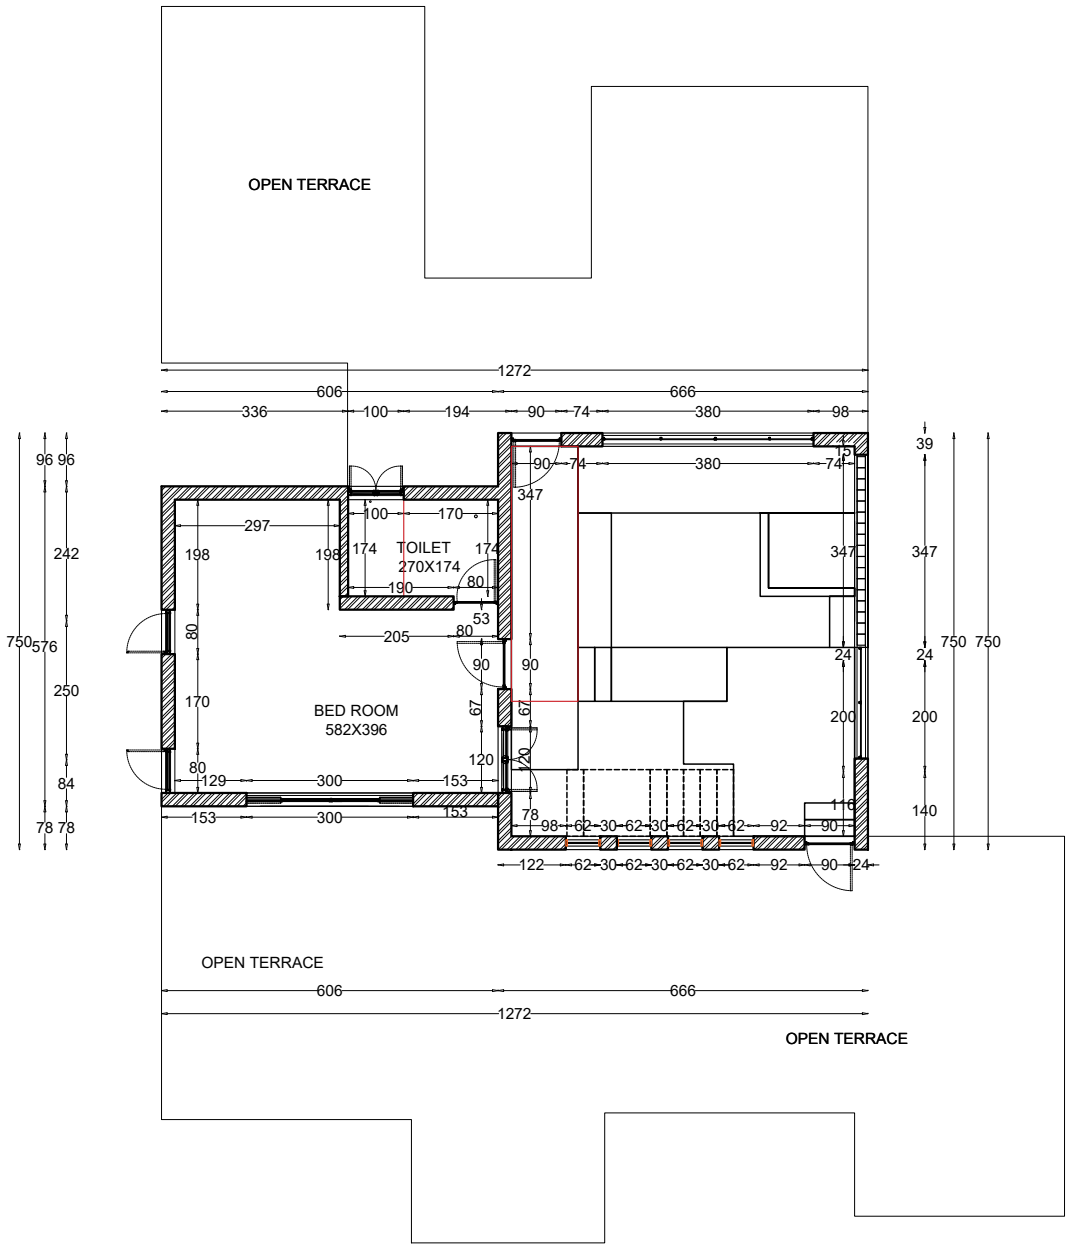


07 **MEASUREMENT**
FIRST FLOOR
SCALE 1:100

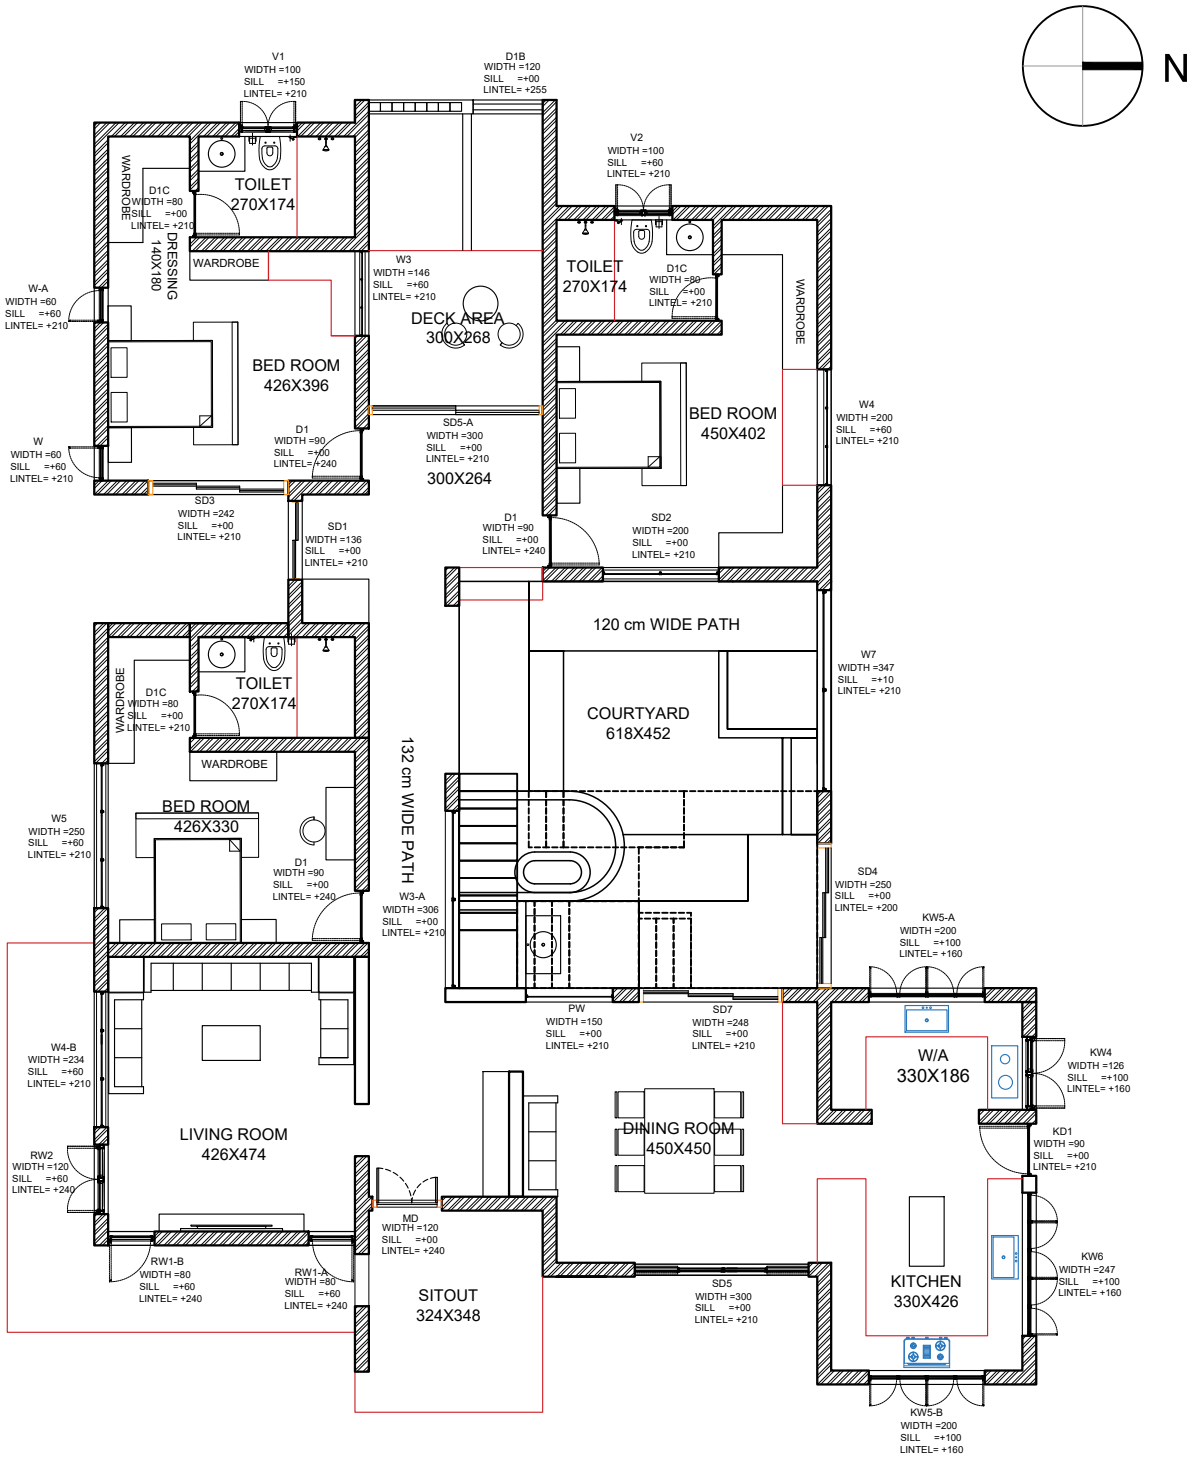


OPENING SCHEDULE - GROUND FLOOR AND FIRST FLOOR						
NO	ITHEM		SIZE	GF	FF	TOTAL
1	DOOR	MD	120 X 240	1	0	1
2	DOOR D1	D1	90 X 240	3	2	5
3	DOOR D1A	D1A	90 X 210	0	1	1
4	KITCHEN DOOR KD1	KD1	90 X 210	1	0	1
5	DOOR D1B	D1B	120 X 255	1	0	1
6	DOOR D1C	D1C	80 X 210	3	1	4
7	WINDOW W,W-A	W,W-A	60 X 150	2	0	2
8	WINDOW RW1-A,RW1-B	RW1	80 X 240	2	0	2
9	WINDOW RW2	RW2	120 X 240	1	0	1
10	WINDOW RW2-A,RW2-B	RW2	80 X 270	0	2	2
11	WINDOW RW2C	RW2	120 X 210	0	1	1
12	WINDOW W3	W3	146 X 150	1	1	1
13	PLAIN WINDOW PW	PW	150 X 210	1	0	1
14	WINDOW W4	W4	200 X 150	1	0	1
15	WINDOW W4A	W4A	220 X 140	0	1	1
16	WINDOW W4B	W4B	234 X 150	1	0	1
17	WINDOW W5	W5	250 X 150	1	1	2
18	WINDOW W3A	W3A	306 X 210	1	0	1
19	WINDOW W6	W6	350 X 260	0	1	1
20	WINDOW W7	W7	347 X 200	1	0	1
21	WINDOW KW4	KW4	126 X 60	1	0	1
22	WINDOW KW5A,KW5B	KW5	200 X 60	2	0	2
23	WINDOW KW6	KW6	247 X 60	1	0	1
24	R WINDOW,W1,W2,W3,W4	RW	62 X 165	0	4	4
25	SLIDING DOOR SD1	SD1	136 X 210	1	0	1
26	SLIDING DOOR SD2	SD2	200 X 210	1	0	1
27	SLIDING DOOR SD3	SD3	242 X 210	1	0	1
28	SLIDING DOOR SD4	SD4	250 X 200	1	0	1
29	SLIDING DOOR SD5,SD5-A	SD5	300X 210	2	0	2
30	SLIDING DOOR RSD6	RSD6	300 X 280	0	1	1
31	SLIDING DOOR SD7	SD7	248 X 210	1	0	1
32	VENTLATION V1,V2,V3	V	100 X 60	2	1	3

08 **SILL-LINTEL**
FIRST FLOOR
SCALE 1:100

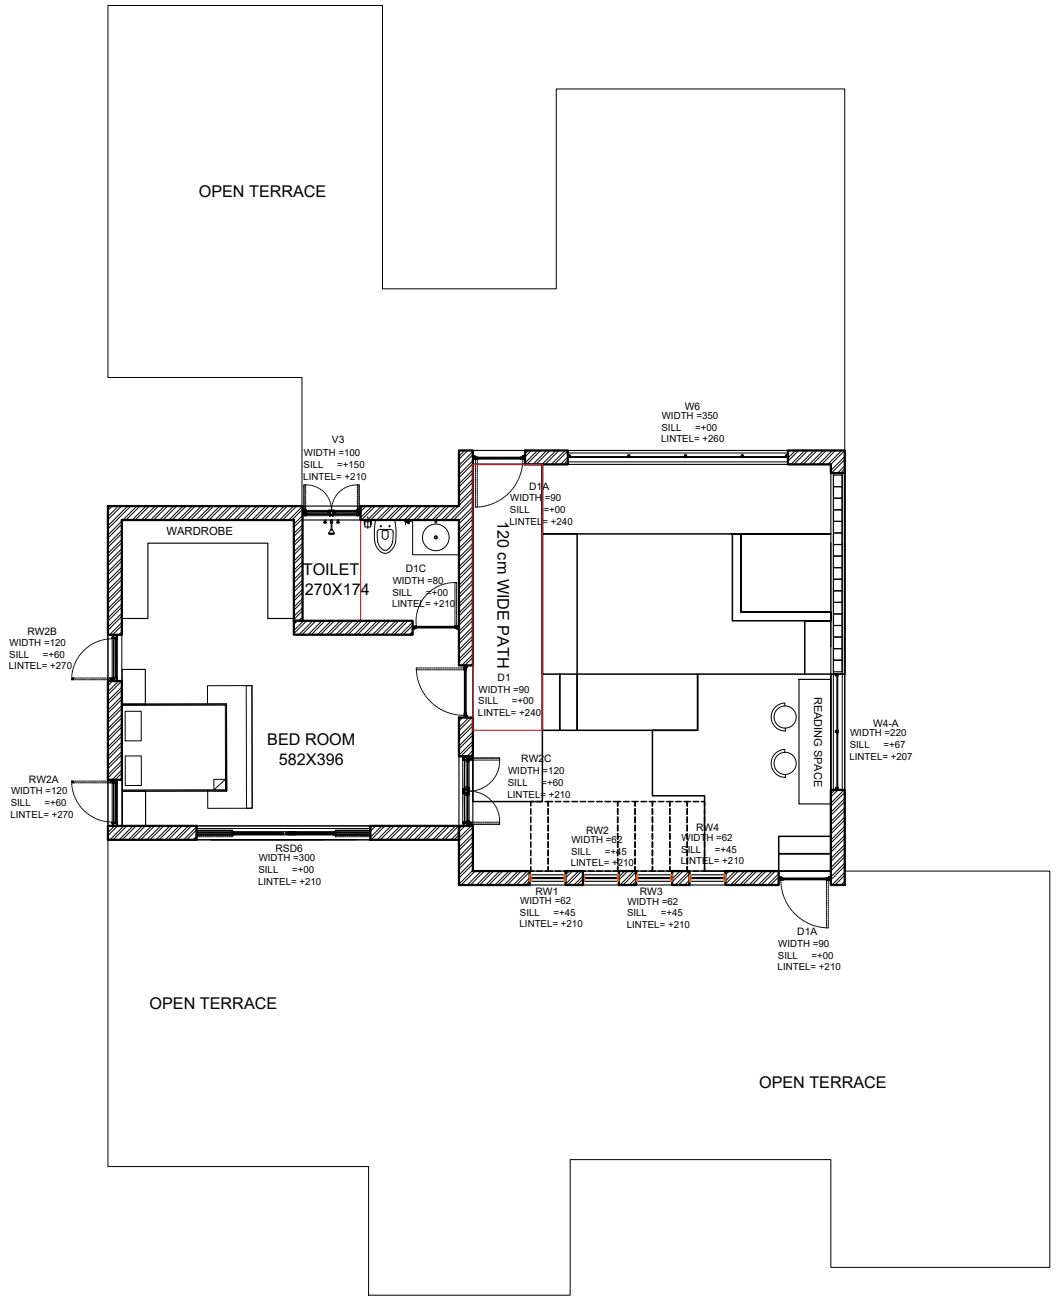


OPENING SCHEDULE - GROUND FLOOR AND FIRST FLOOR						
NO	ITHEM		SIZE	GF	FF	TOTAL
1	DOOR	MD	120 X 240	1	0	1
2	DOOR D1	D1	90 X 240	3	2	5
3	DOOR D1A	D1A	90 X 210	0	1	1
4	KITCHEN DOOR KD1	KD1	90 X 210	1	0	1
5	DOOR D1B	D1B	120 X 255	1	0	1
6	DOOR D1C	D1C	80 X 210	3	1	4
7	WINDOW W,W-A	W,W-A	60 X 150	2	0	2
8	WINDOW RW1-A,RW1-B	RW1	80 X 240	2	0	2
9	WINDOW RW2	RW2	120 X 240	1	0	1
10	WINDOW RW2-A,RW2-B	RW2	80 X 270	0	2	2
11	WINDOW RW2C	RW2	120 X 210	0	1	1
12	WINDOW W3	W3	146 X 150	1	1	1
13	PLAIN WINDOW PW	PW	150 X 210	1	0	1
14	WINDOW W4	W4	200 X 150	1	0	1
15	WINDOW W4A	W4A	220 X 140	0	1	1
16	WINDOW W4B	W4B	234 X 150	1	0	1
17	WINDOW W5	W5	250 X 150	1	1	2
18	WINDOW W3A	W3A	306 X 210	1	0	1
19	WINDOW W6	W6	350 X 260	0	1	1
20	WINDOW W7	W7	347 X 200	1	0	1
21	WINDOW KW4	KW4	126 X 60	1	0	1
22	WINDOW KW5A,KW5B	KW5	200 X 60	2	0	2
23	WINDOW KW6	KW6	247 X 60	1	0	1
24	R WINDOW,W1,W2,W3,W4	RW	62 X 165	0	4	4
25	SLIDING DOOR SD1	SD1	136 X 210	1	0	1
26	SLIDING DOOR SD2	SD2	200 X 210	1	0	1
27	SLIDING DOOR SD3	SD3	242 X 210	1	0	1
28	SLIDING DOOR SD4	SD4	250 X 200	1	0	1
29	SLIDING DOOR SD5,SD5-A	SD5	300X 210	2	0	2
30	SLIDING DOOR RSD6	RSD6	300 X 280	0	1	1
31	SLIDING DOOR SD7	SD7	248 X 210	1	0	1
32	VENTLATION V1,V2,V3	V	100 X 60	2	1	3


08 **SILL-LINTEL**
FIRST FLOOR
SCALE 1:100

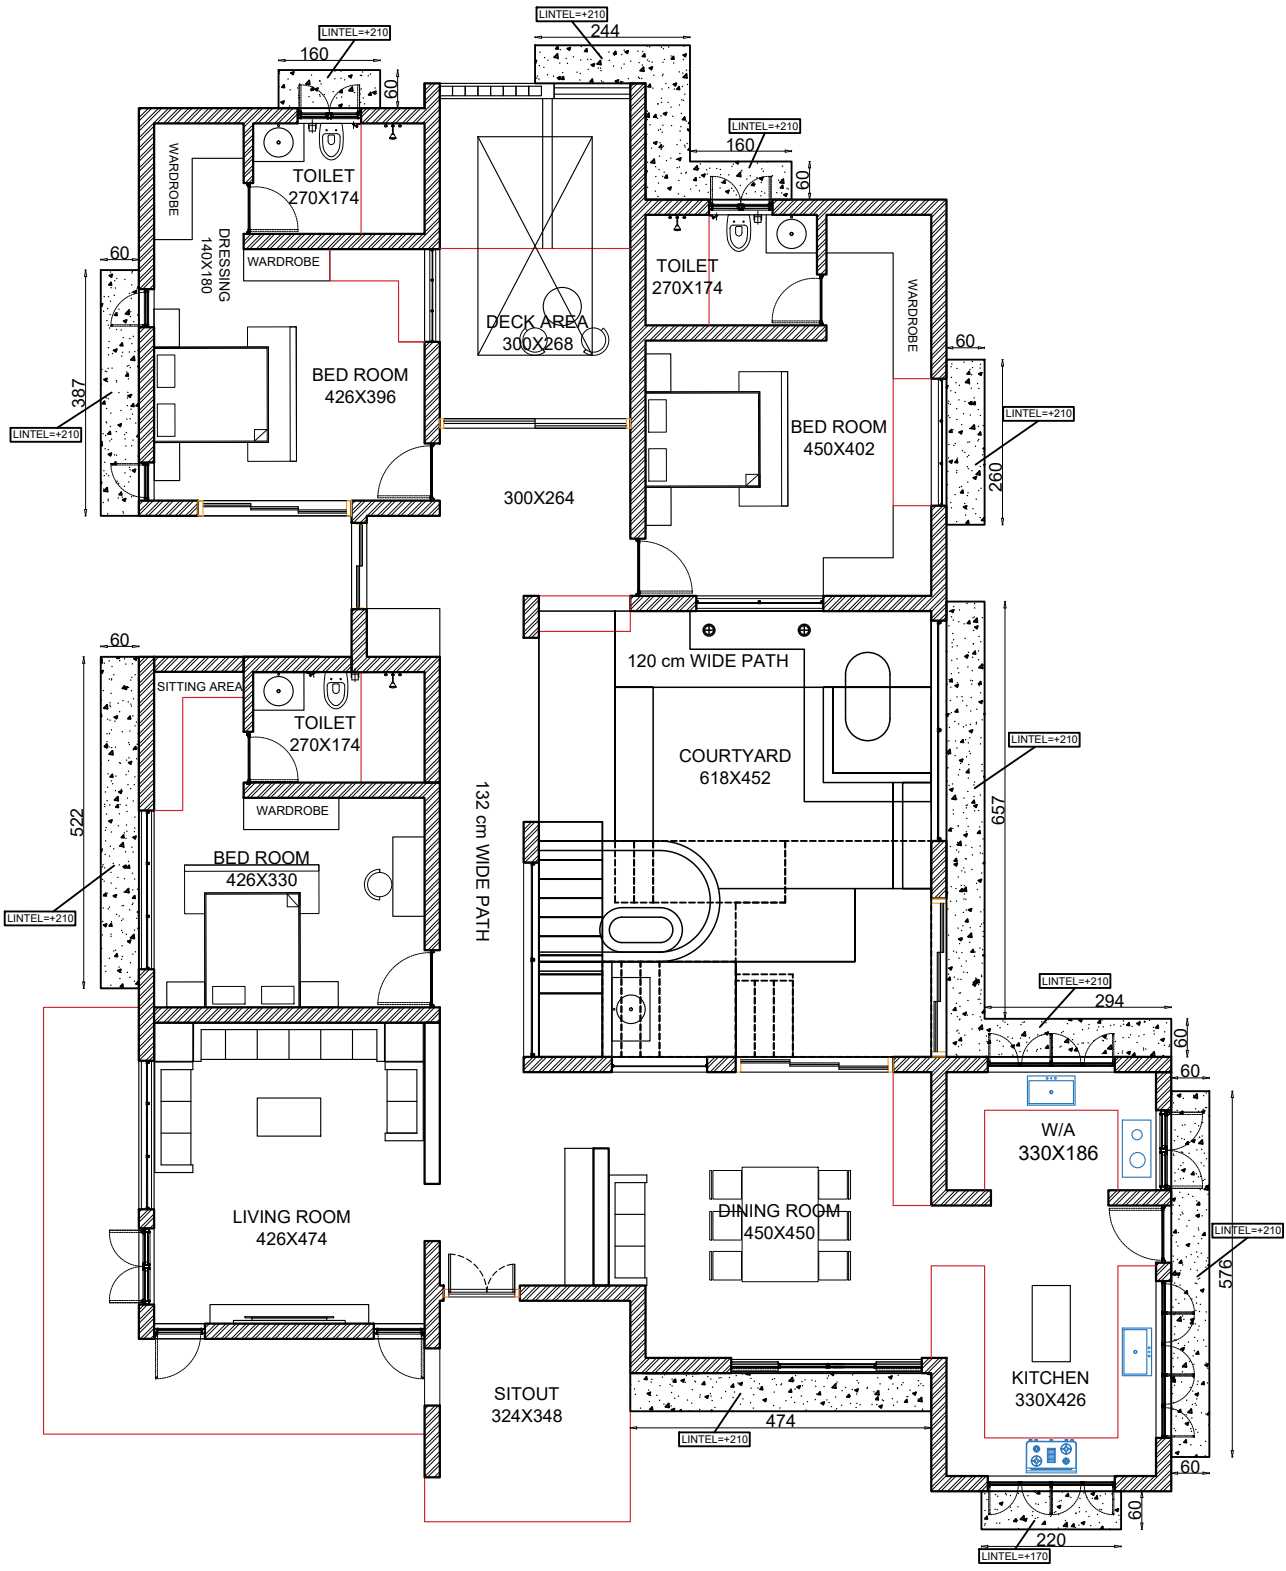


09 **LINTEL SLAB DRAWING**
GROUND FLOOR
SCALE 1:100

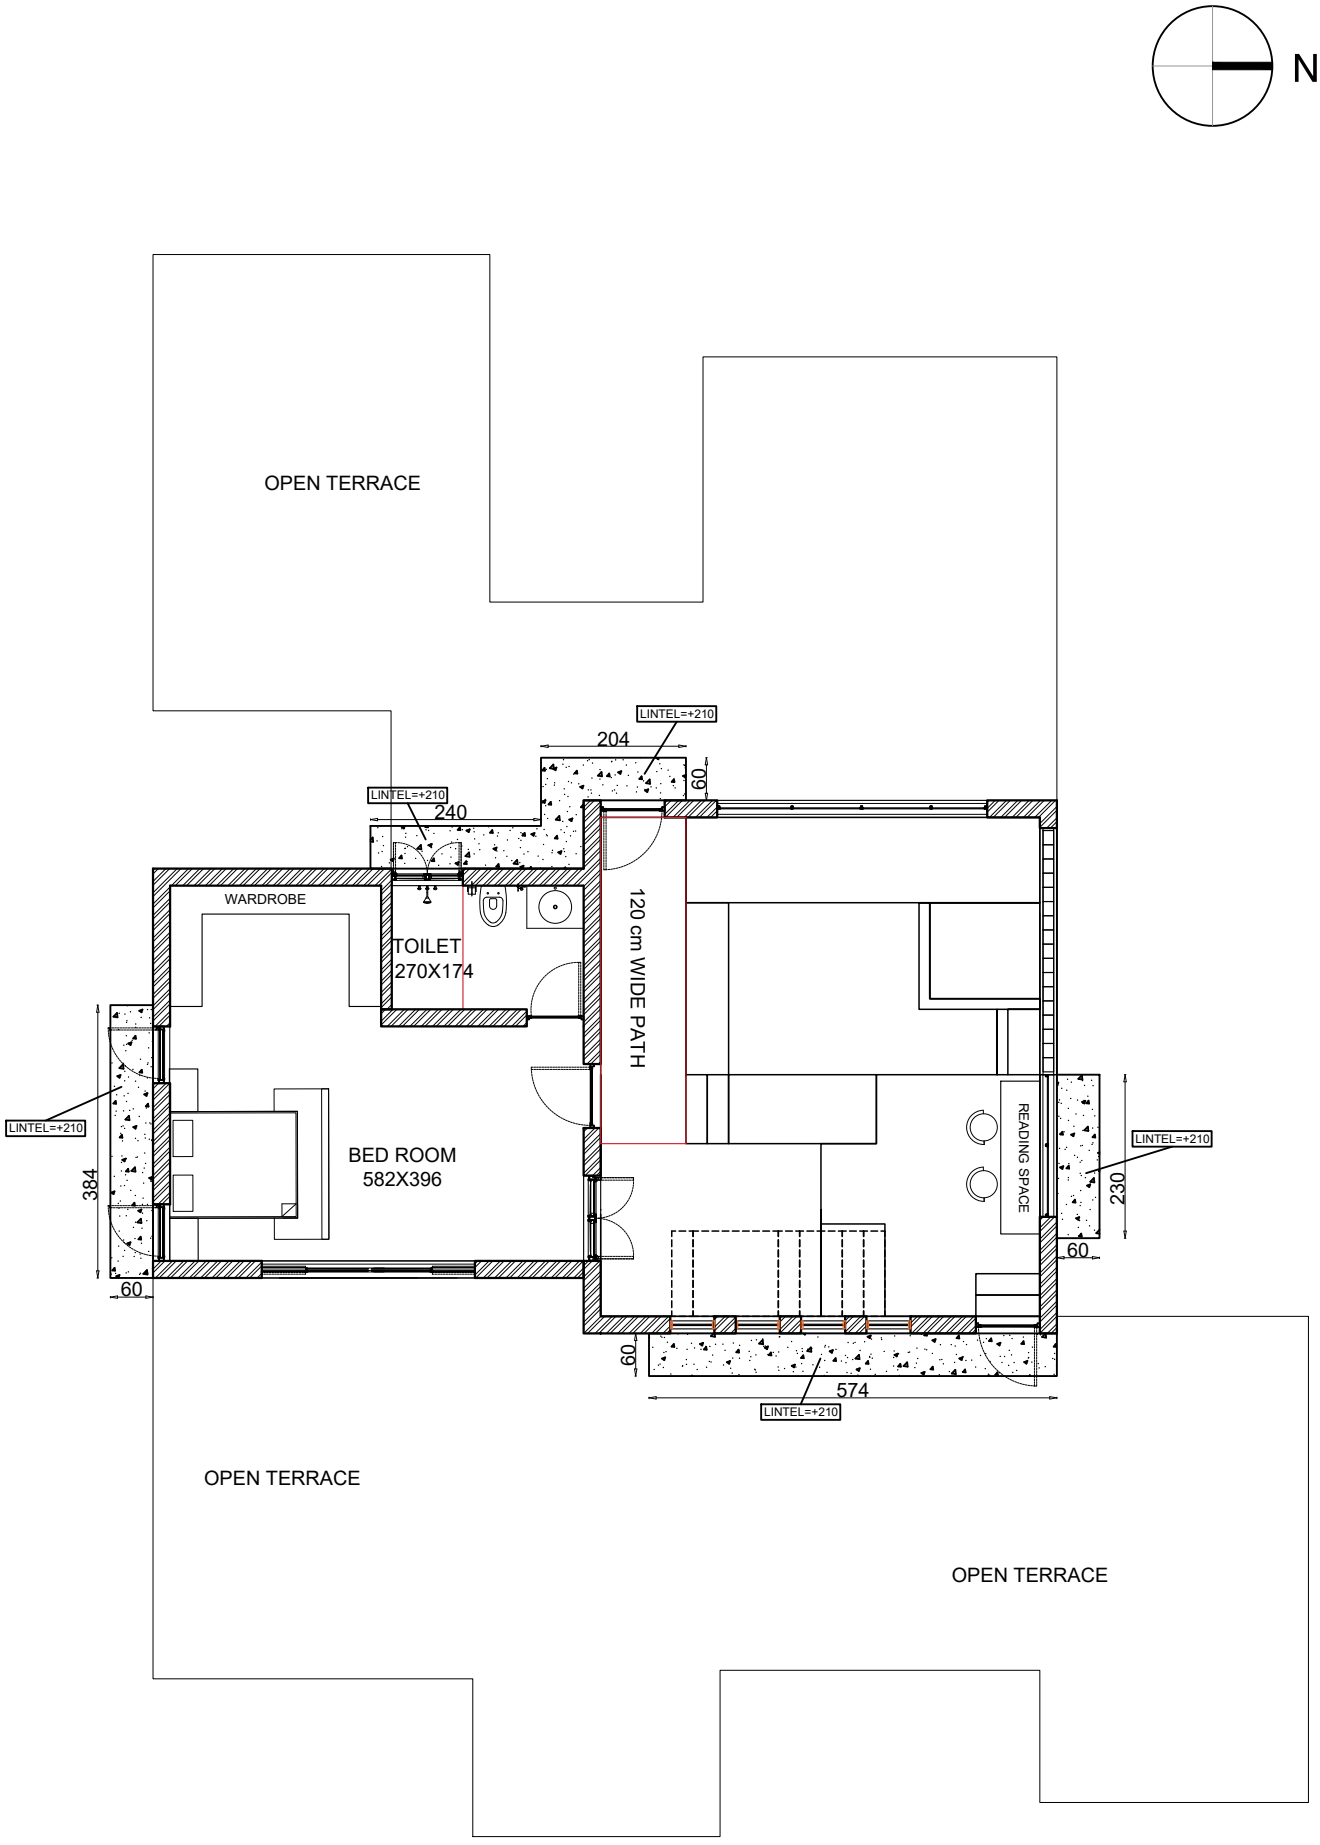


09 LINTEL SLAB DRAWING
FIRST FLOOR
SCALE 1:100

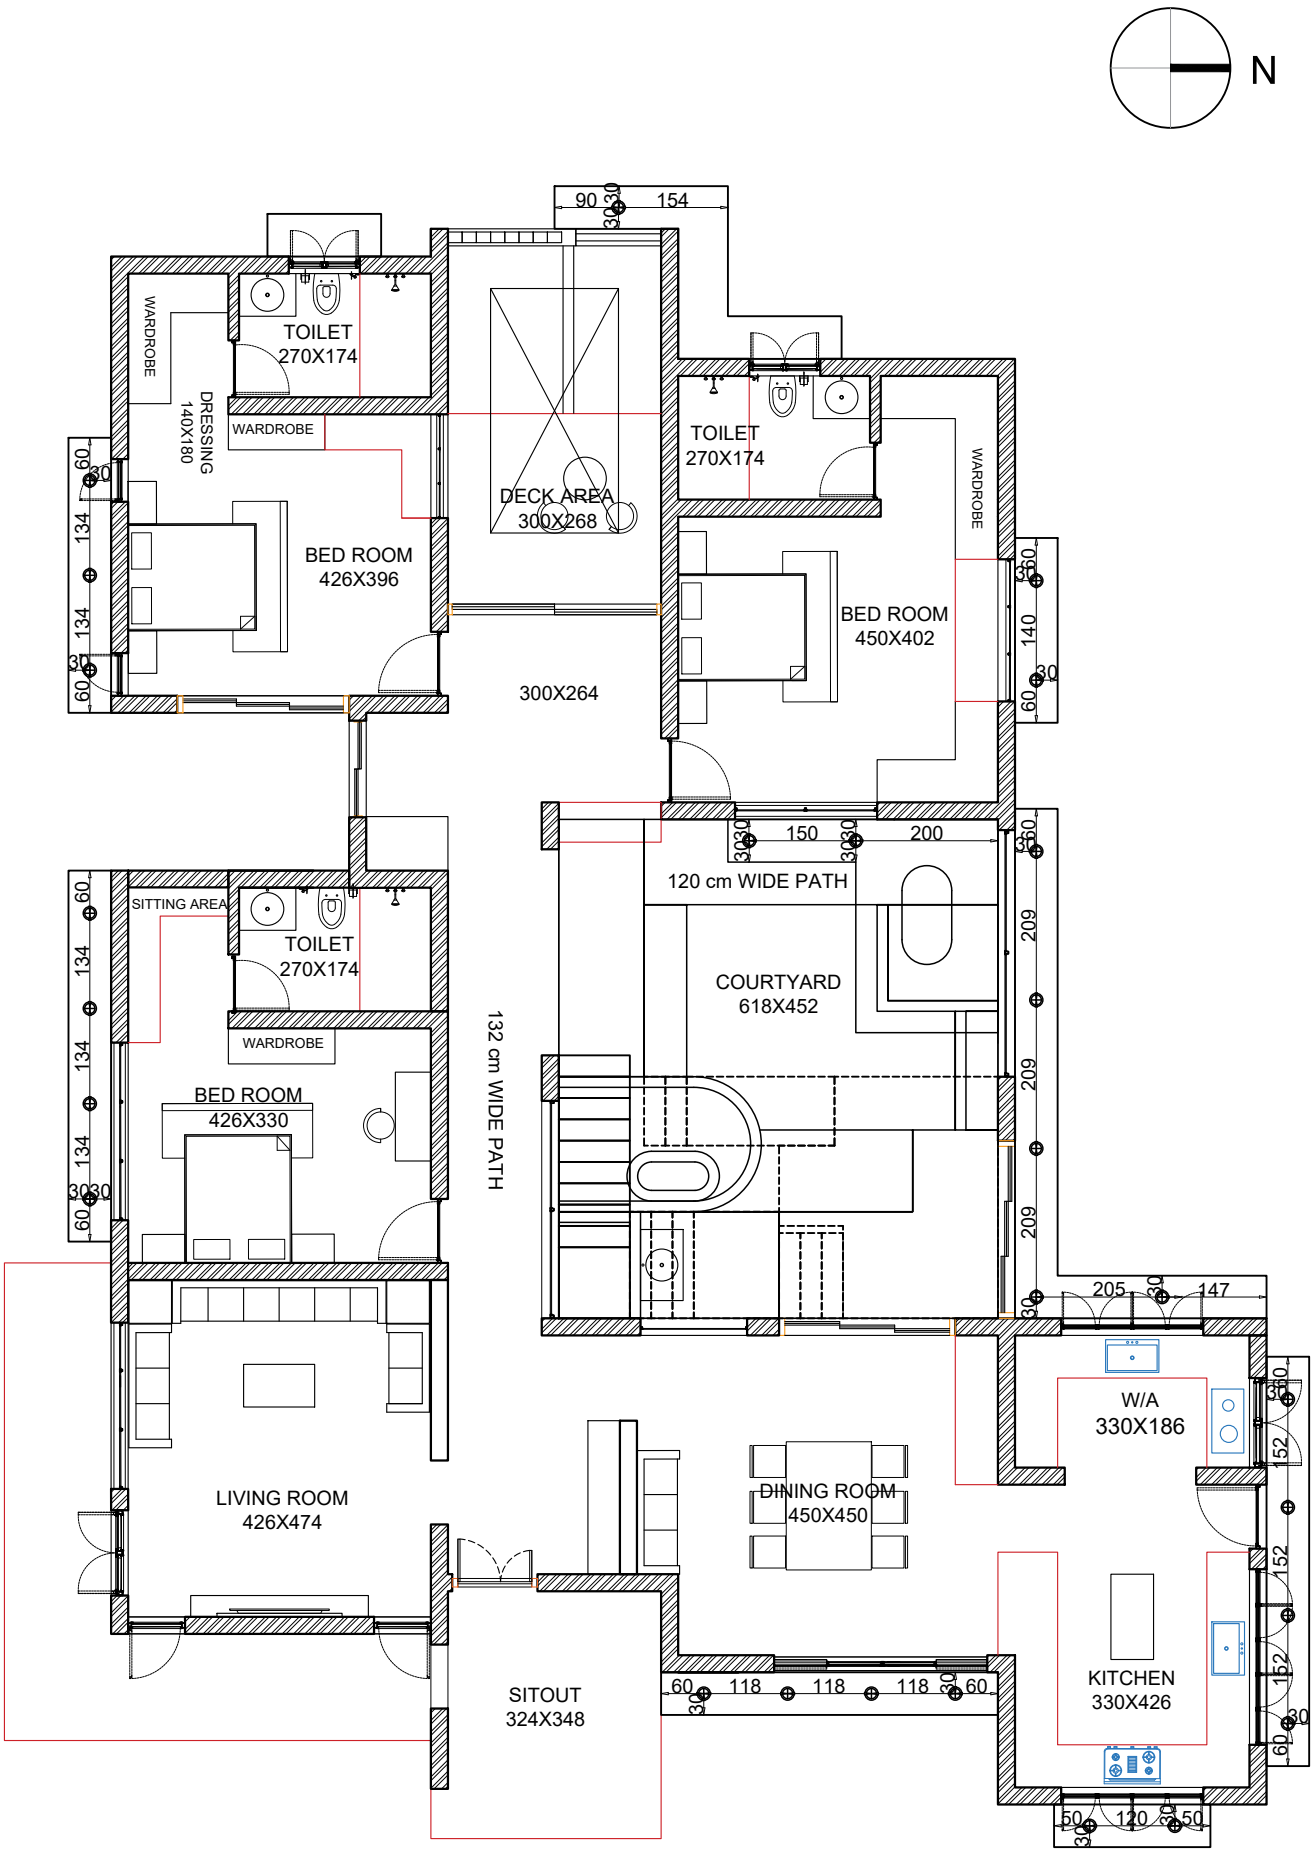



09 LINTEL POINT SLAB
GROUND FLOOR
SCALE 1:100

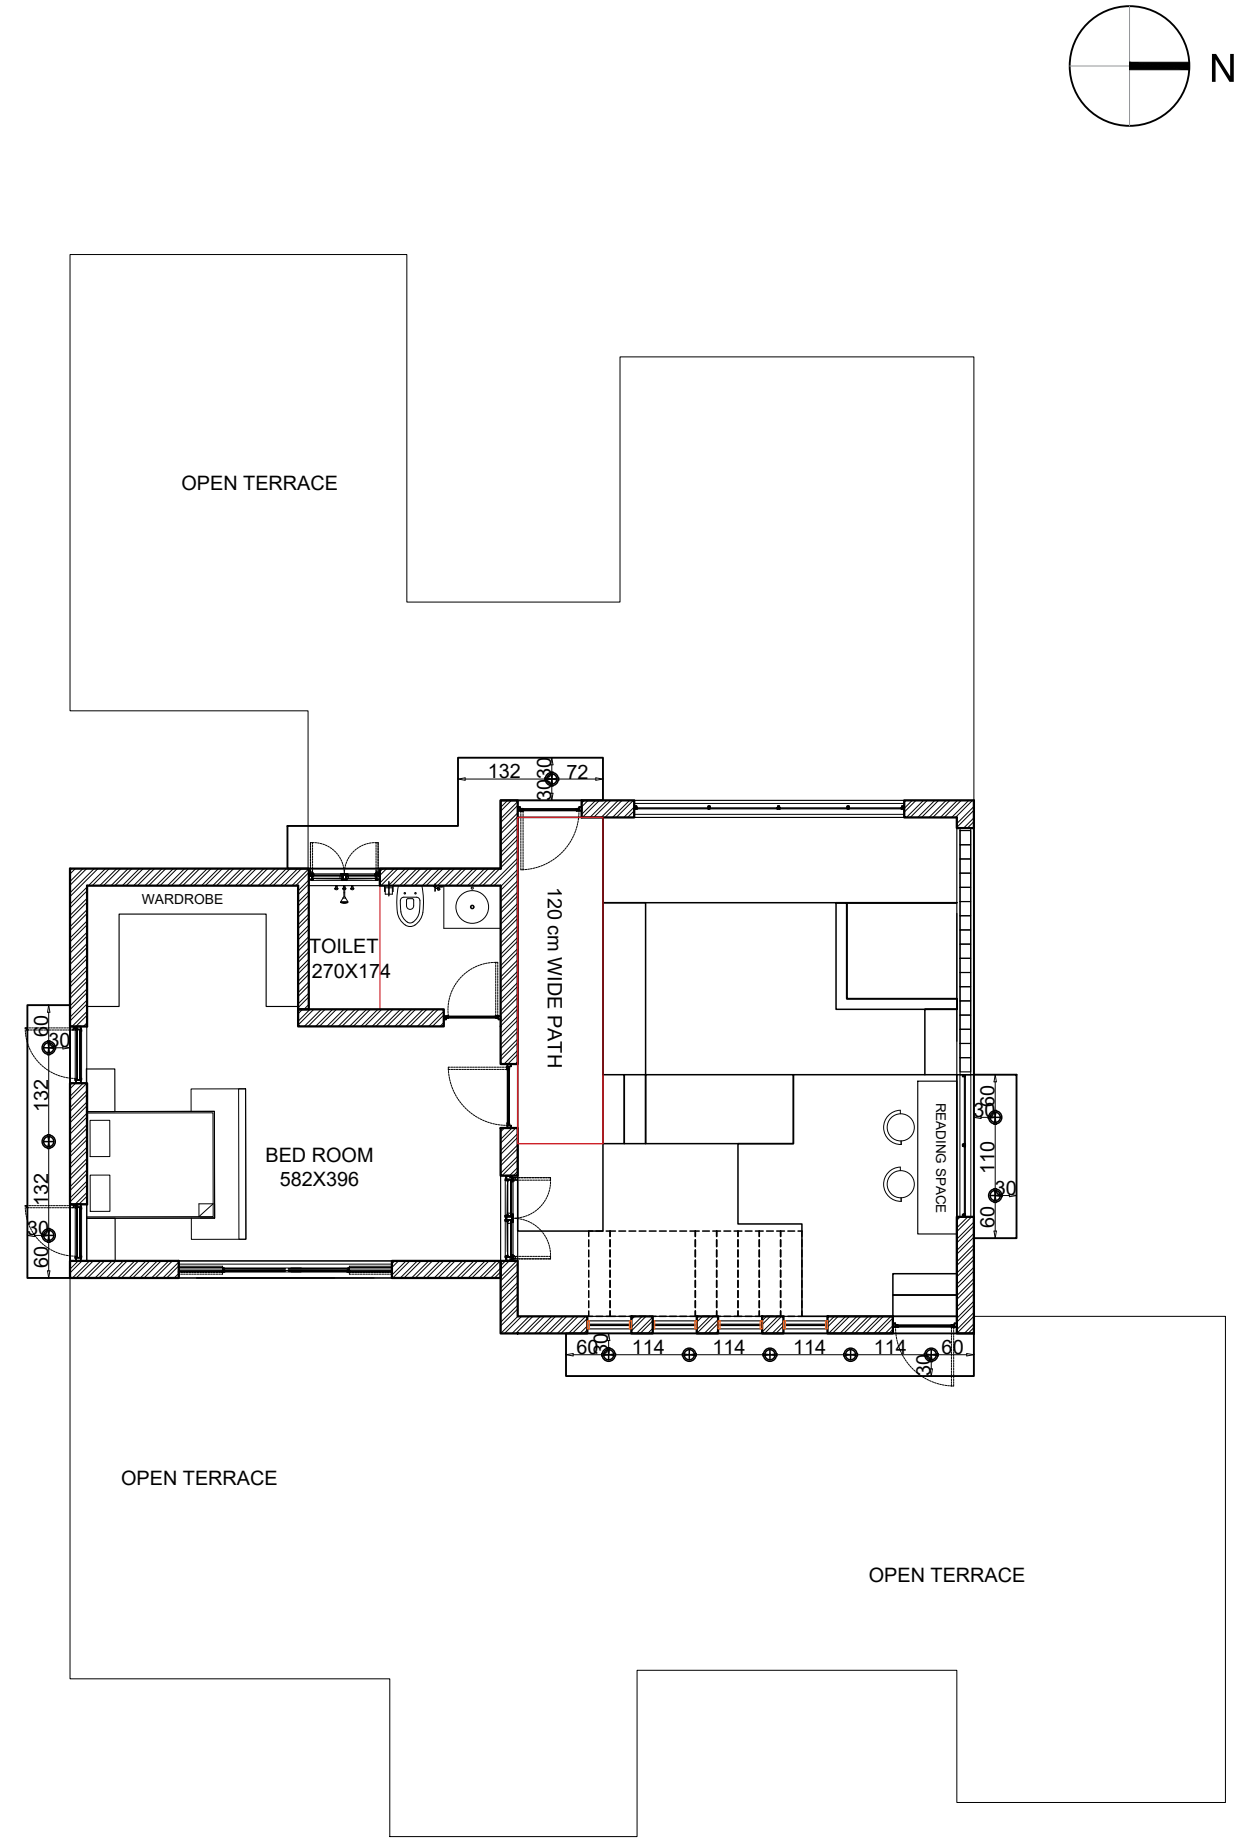


09 **LINTEL POINT SLAB**
FIRST FLOOR
SCALE 1:100

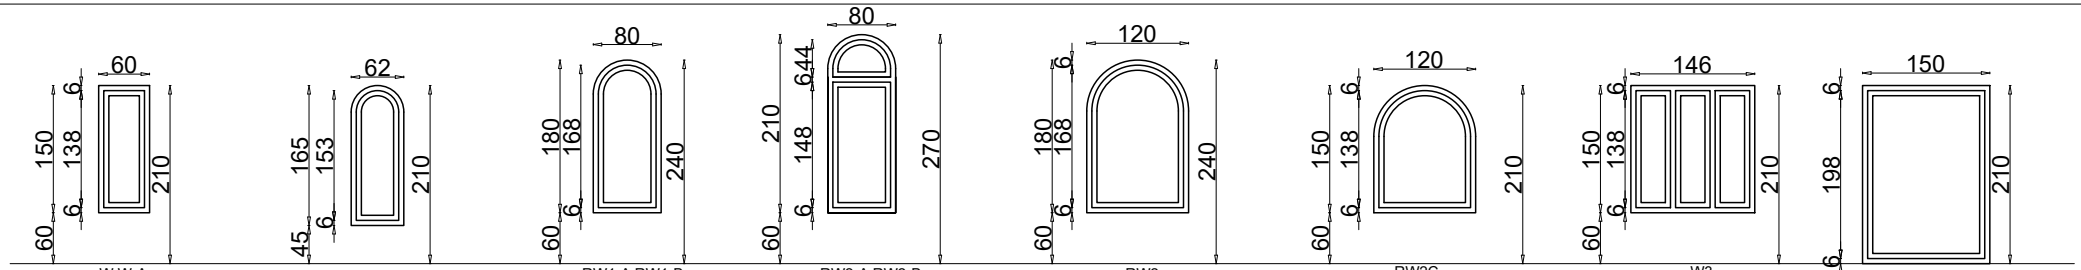

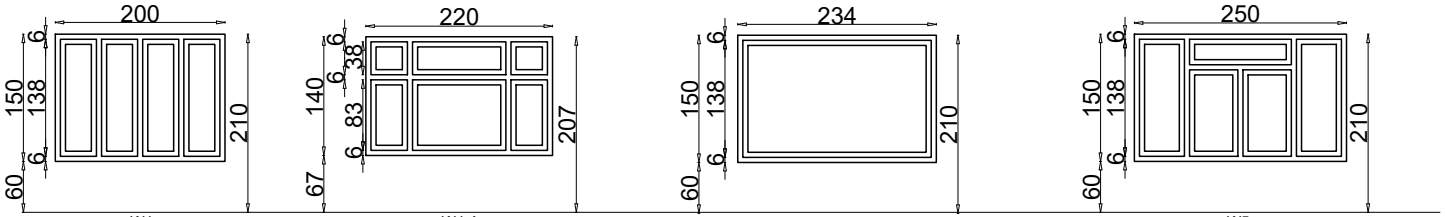

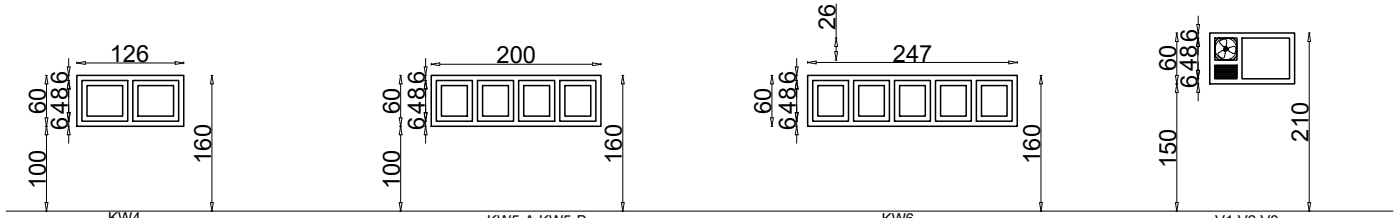


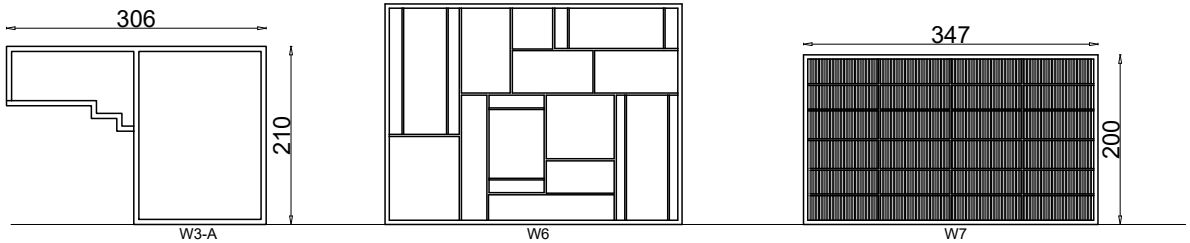



10 WINDOW SCHEDULE
SCALE 1:100

OPENING SCHEDULE - GROUND FLOOR AND FIRST FLOOR

NO	ITHEM		SIZE	GF	FF	TOTAL
1	DOOR	MD	120 X 240	1	0	1
2	DOOR D1	D1	90 X 240	3	2	5
3	DOOR D1A	D1A	90 X 210	0	1	1
4	KITCHEN DOOR KD1	KD1	90 X 210	1	0	1
5	DOOR D1B	D1B	120 X 255	1	0	1
6	DOOR D1C	D1C	80 X 210	3	1	4
7	WINDOW W,W-A	W,W-A	60 X 150	2	0	2
8	WINDOW RW1-A,RW1-B	RW1	80 X 240	2	0	2
9	WINDOW RW2	RW2	120 X 240	1	0	1
10	WINDOW RW2-A,RW2-B	RW2	80 X 270	0	2	2
11	WINDOW RW2C	RW2	120 X 210	0	1	1
12	WINDOW W3	W3	146 X 150	1	1	1
13	PLAIN WINDOW PW	PW	150 X 210	1	0	1
14	WINDOW W4	W4	200 X 150	1	0	1
15	WINDOW W4A	W4A	220 X 140	0	1	1
16	WINDOW W4B	W4B	234 X 150	1	0	1
17	WINDOW W5	W5	250 X 150	1	1	2
18	WINDOW W3A	W3A	306 X 210	1	0	1
19	WINDOW W6	W6	350 X 260	0	1	1
20	WINDOW W7	W7	347 X 200	1	0	1
21	WINDOW KW4	KW4	126 X 60	1	0	1
22	WINDOW KW5A,KW5B	KW5	200 X 60	2	0	2
23	WINDOW KW6	KW6	247 X 60	1	0	1
24	R WINDOW,W1,W2,W3,W4	RW	62 X 165	0	4	4
25	SLIDING DOOR SD1	SD1	136 X 210	1	0	1
26	SLIDING DOOR SD2	SD2	200 X 210	1	0	1
27	SLIDING DOOR SD3	SD3	242 X 210	1	0	1
28	SLIDING DOOR SD4	SD4	250 X 200	1	0	1
29	SLIDING DOOR SD5,SD5-A	SD5	300X 210	2	0	2
30	SLIDING DOOR RSD6	RSD6	300 X 280	0	1	1
31	SLIDING DOOR SD7	SD7	248 X 210	1	0	1
32	VENTLATION V1,V2,V3	V	100 X 60	2	1	3

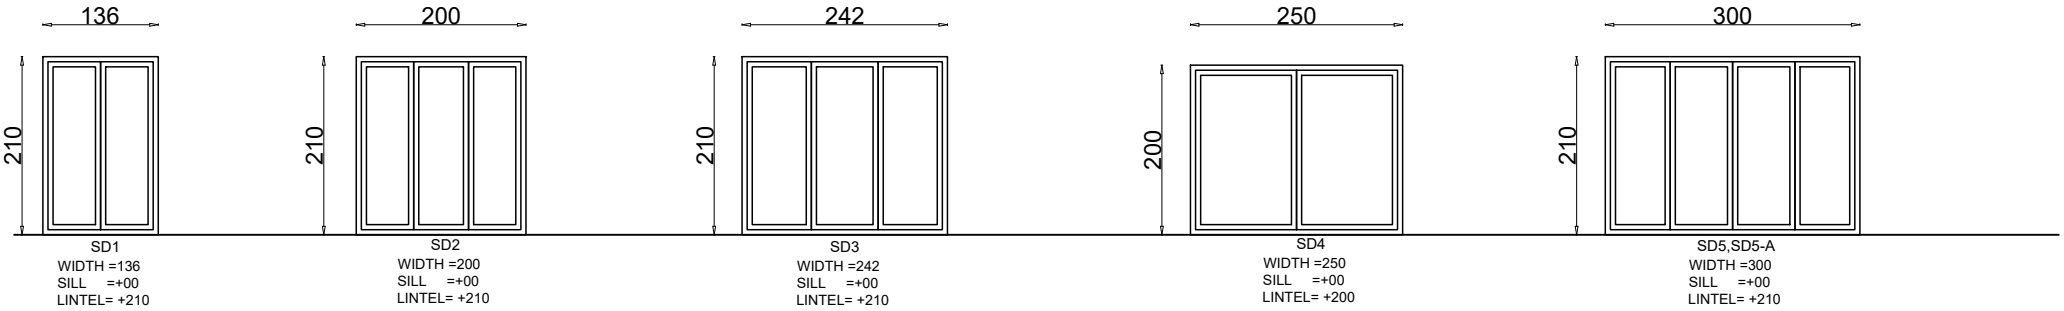


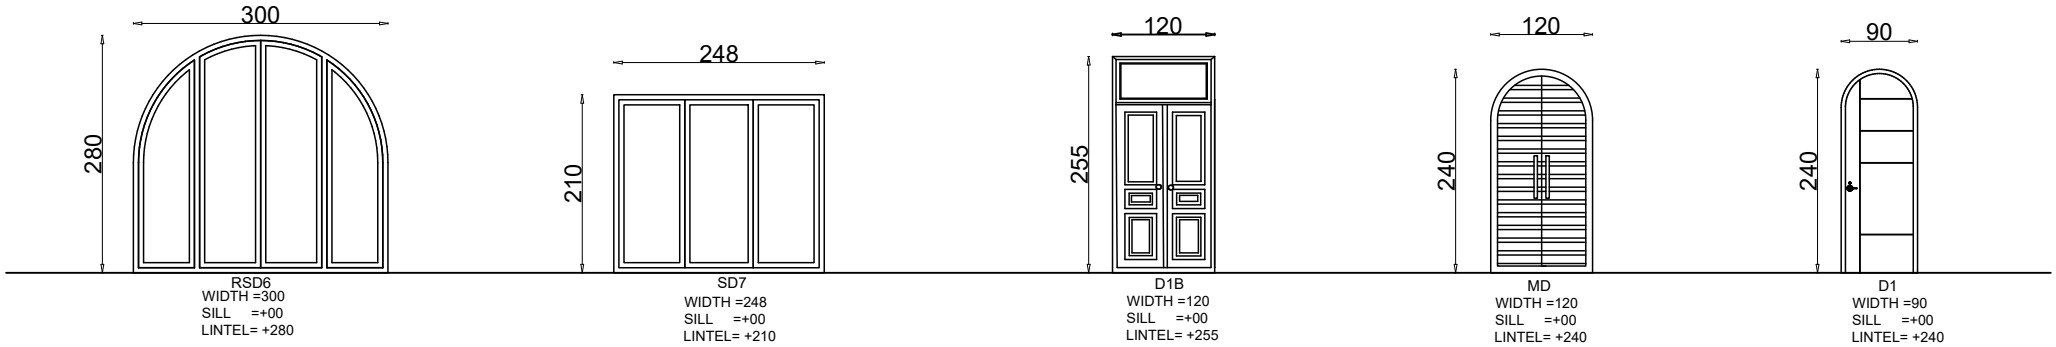

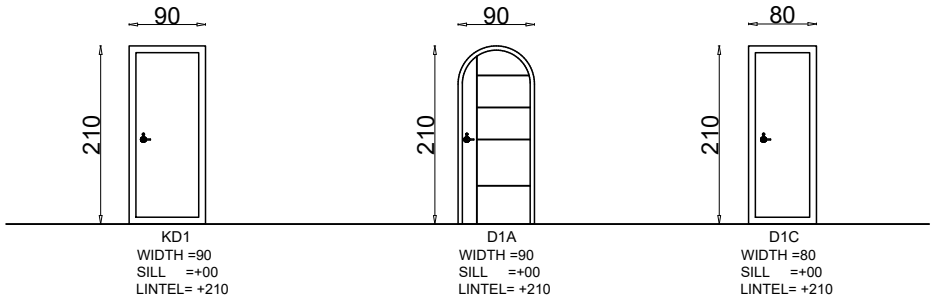


OPENING SCHEDULE - GROUND FLOOR AND FIRST FLOOR						
NO	ITEM		SIZE	GF	FF	TOTAL
1	DOOR	MD	120X240	1	--	1
2	DOOR	D1	90X240	3	2	5
3	DOOR	D1A	90X210	--	1	1
4	DOOR	KD1	90X210	1	--	1
5	DOOR	D1B	120X255	1	--	1
6	DOOR	D1C	80X210	3	1	4
7	SLIDING DOOR	SD1	136X210	1	--	1
8	SLIDING DOOR	SD2	200X210	1	--	1
9	SLIDING DOOR	SD3	242X210	1	--	1
10	SLIDING DOOR	SD4	250X200	1	--	1
11	SLIDING DOOR	SD5,SD5-A	300X210	2	--	2
12	SLIDING DOOR	RSD6	300X280	--	1	1
13	SLIDING DOOR	SD7	248X210	1	--	1

10 **WINDOW SCHEDULE**
SCALE 1:100

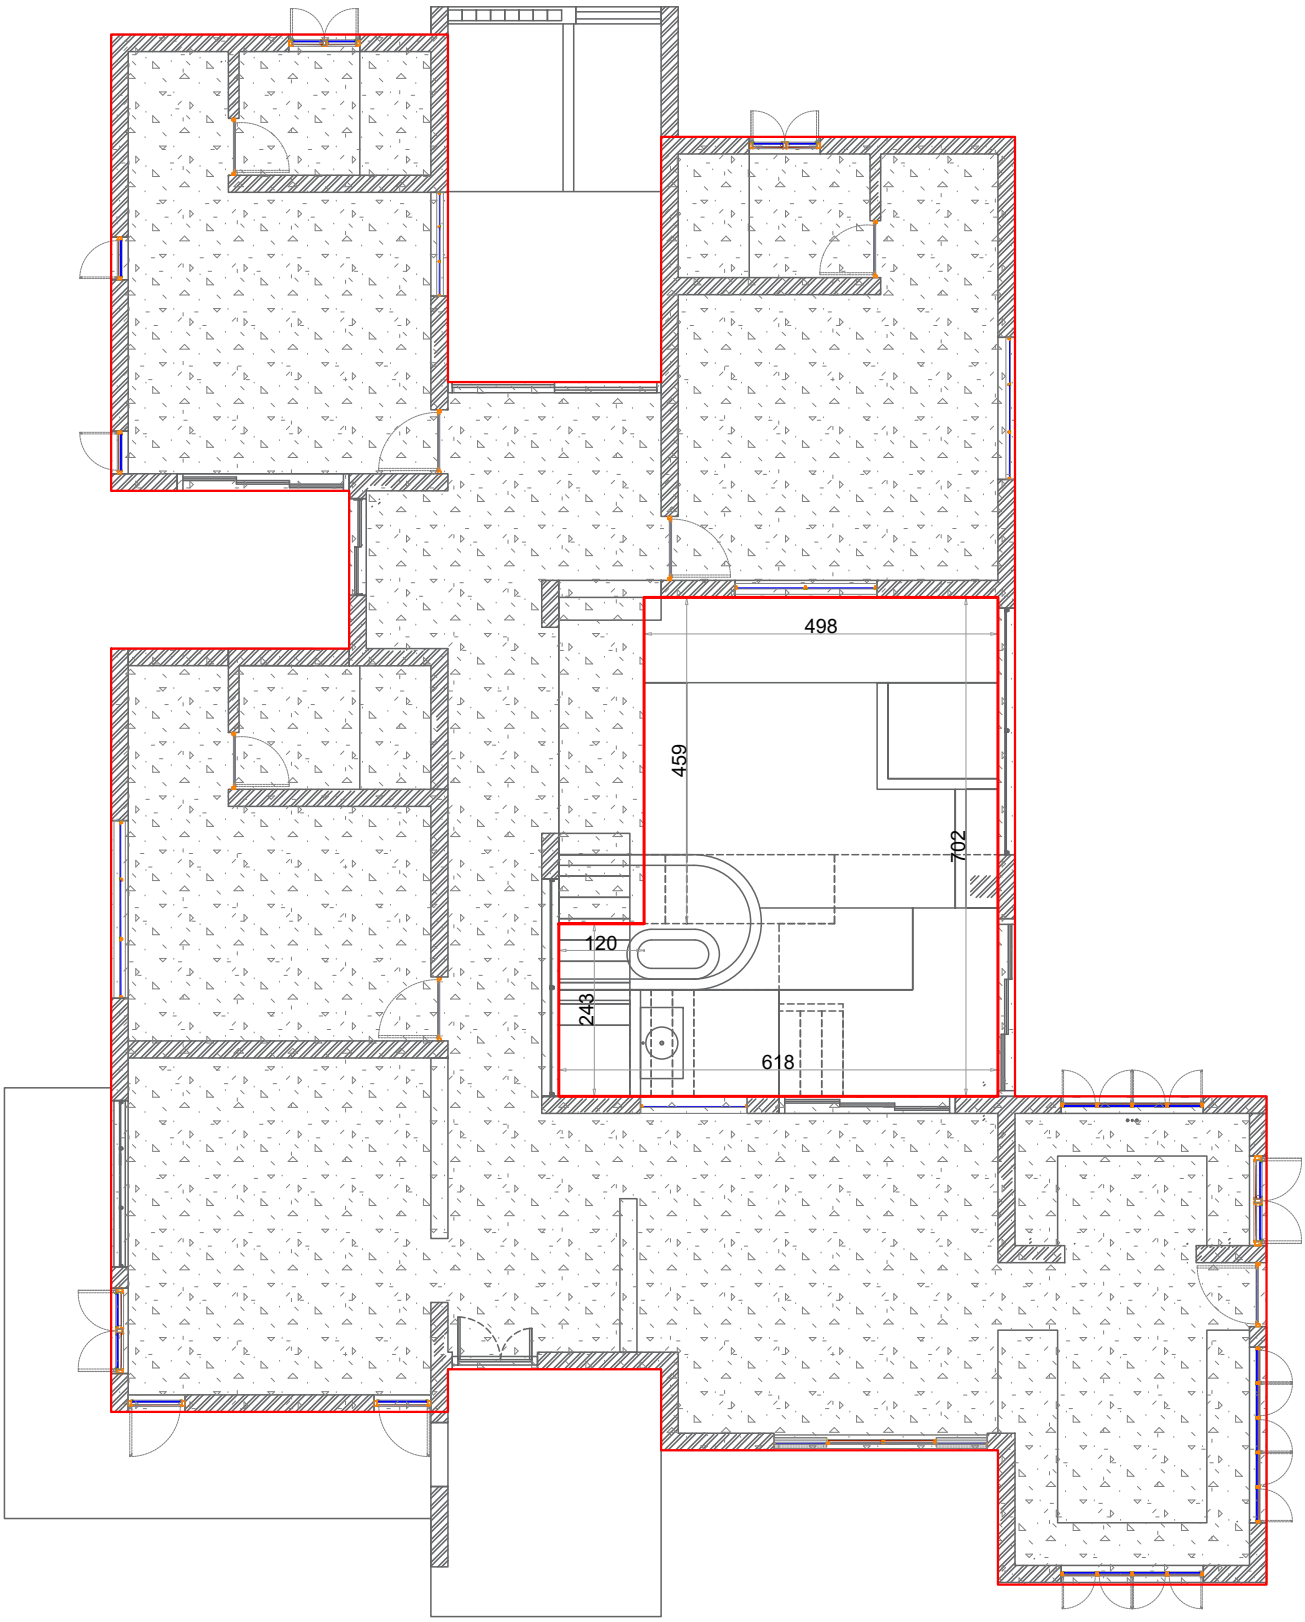


11 SLAB DETAIL GROUND FLOOR


SCALE 1:100

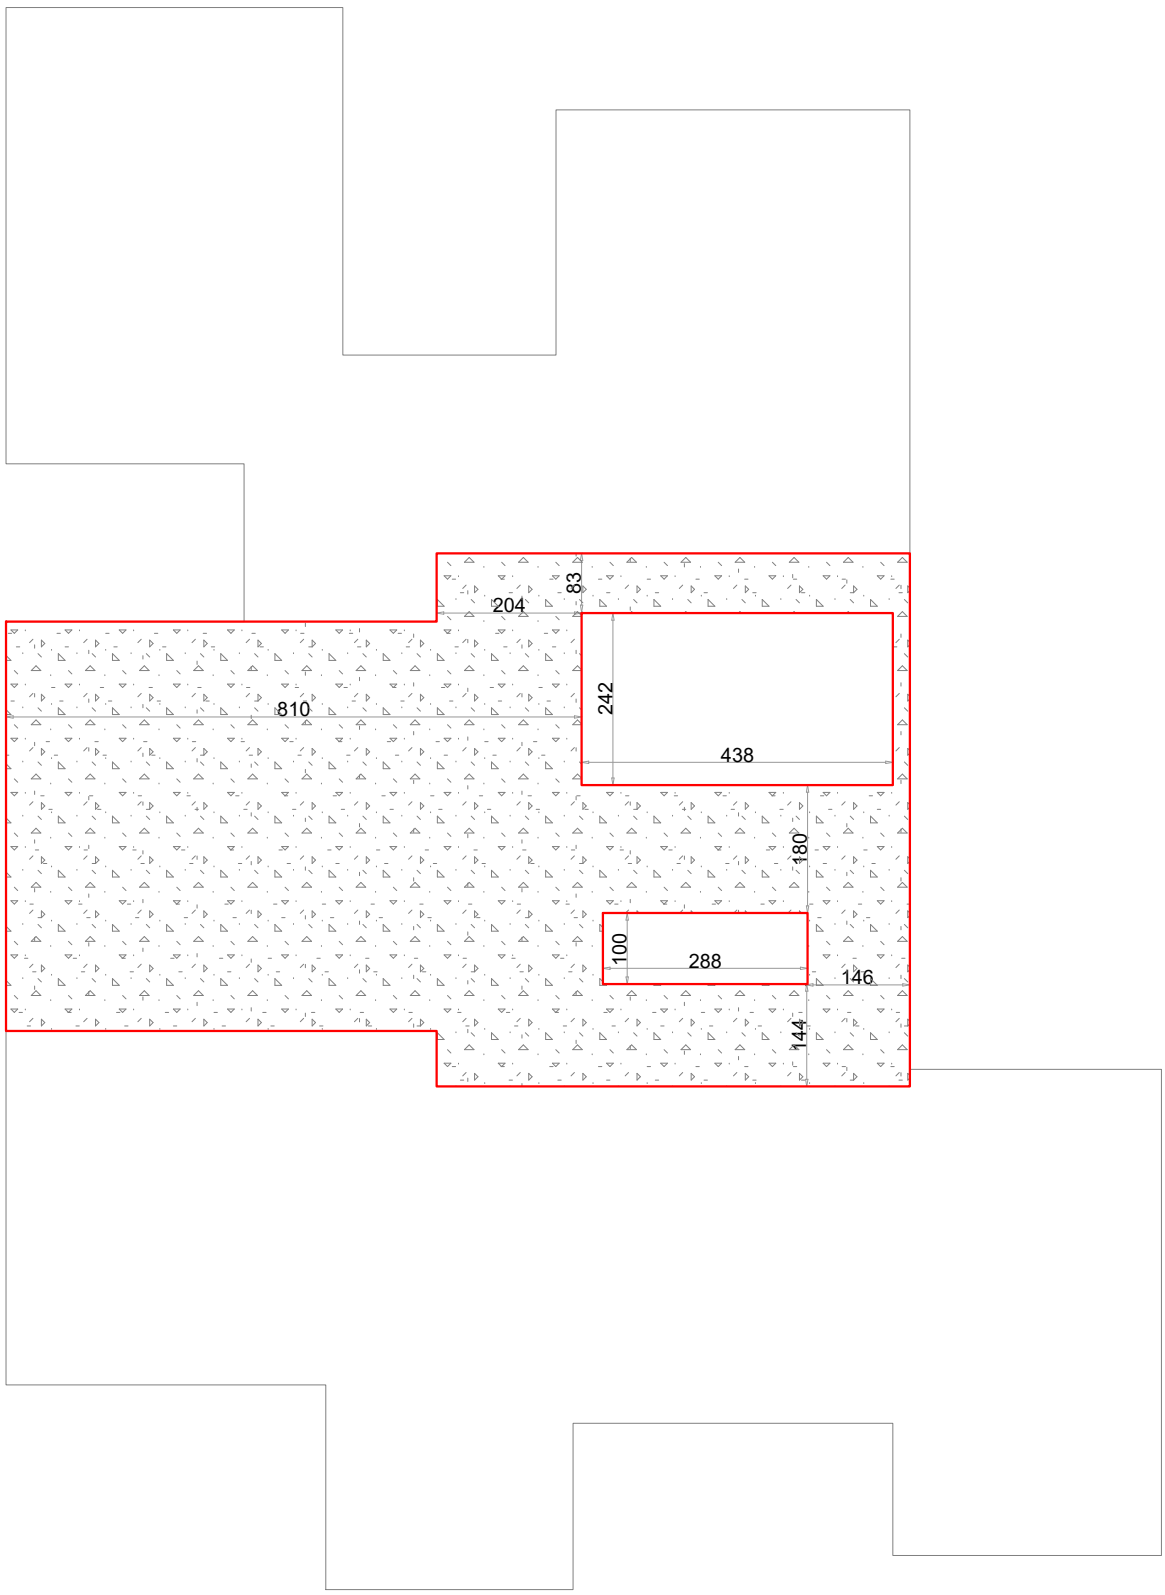


11 SLAB DETAIL
FIRST FLOOR
SCALE 1:100

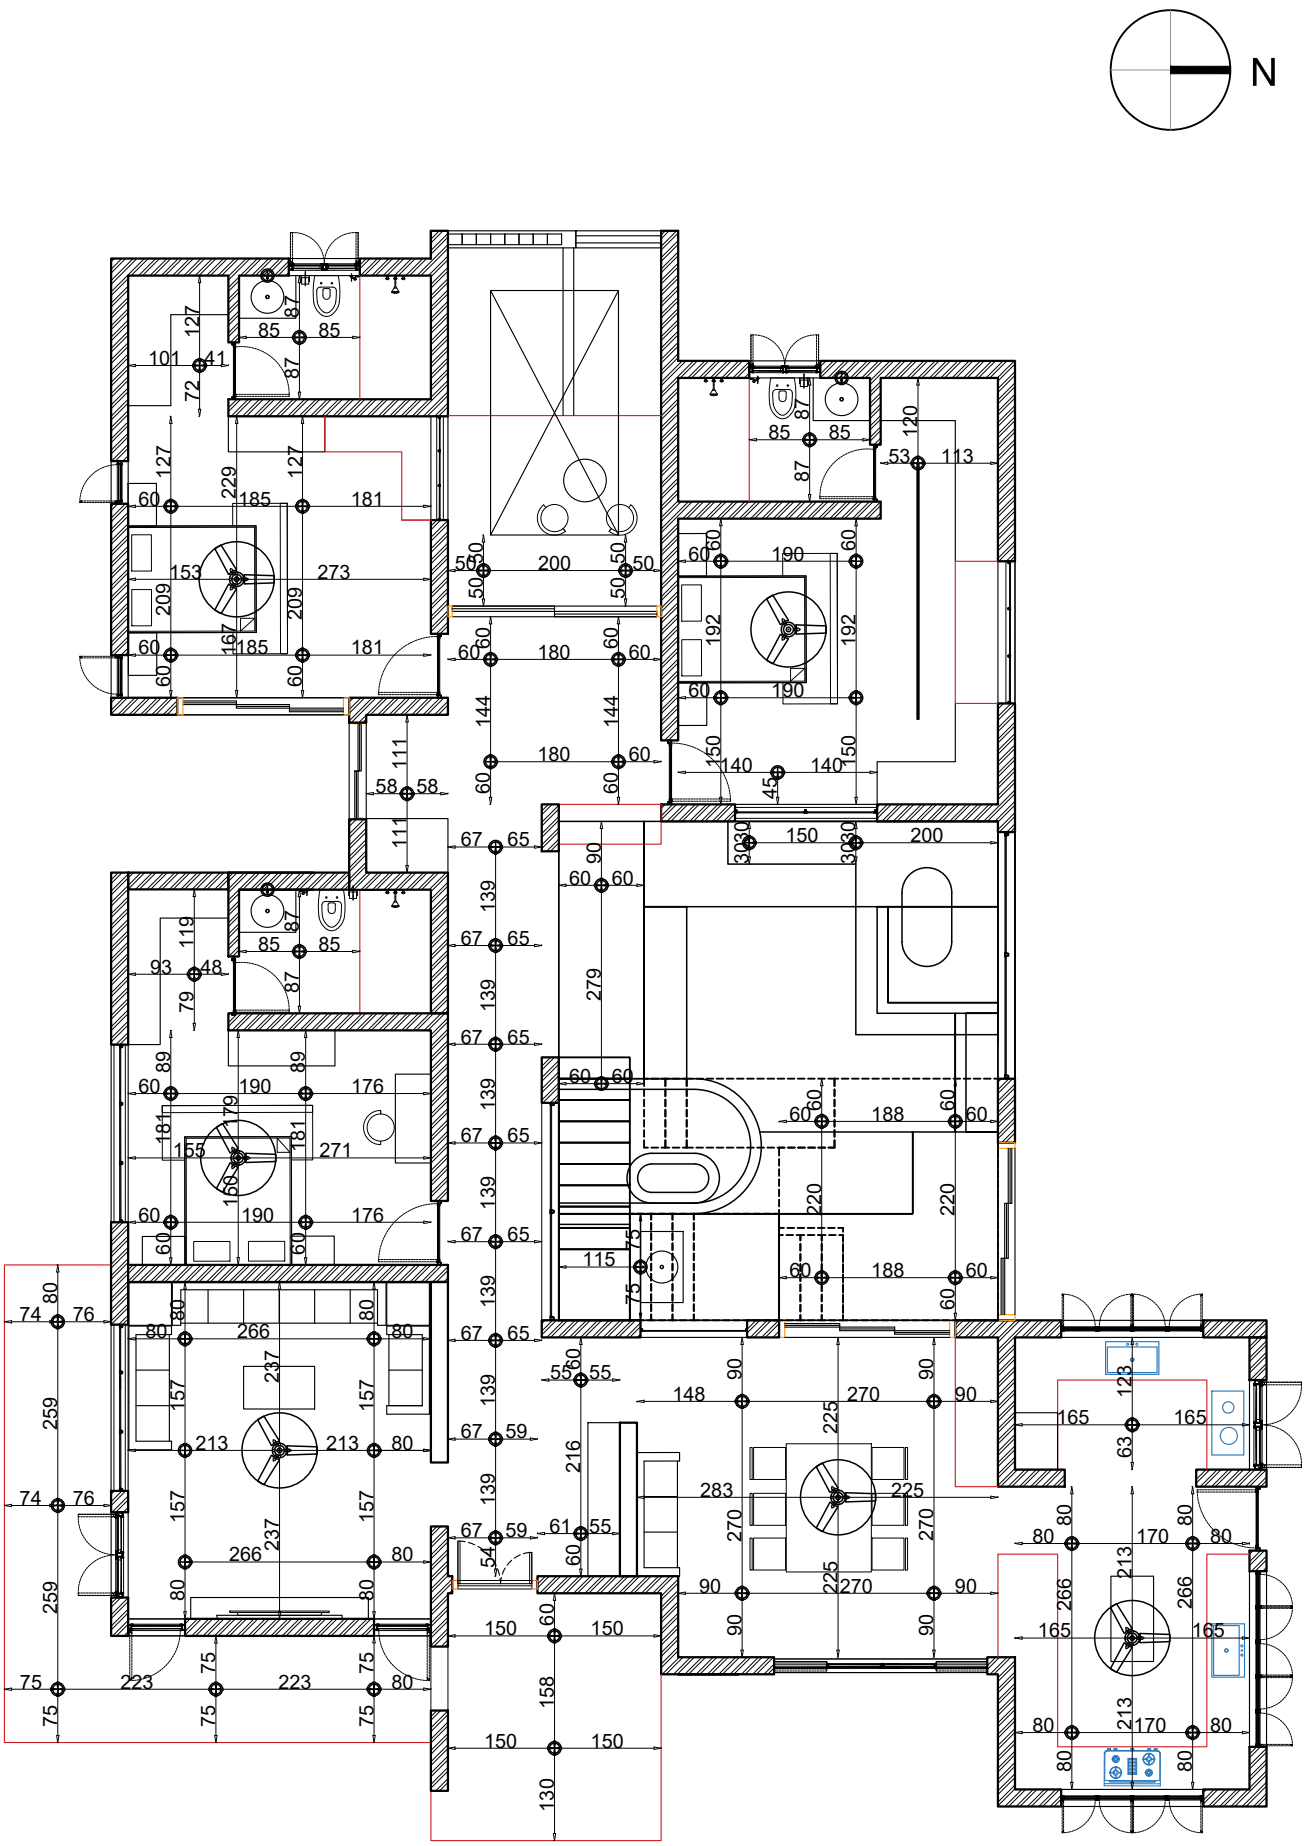

12 **SLAB POINTS**
GROUND FLOOR
SCALE 1:100

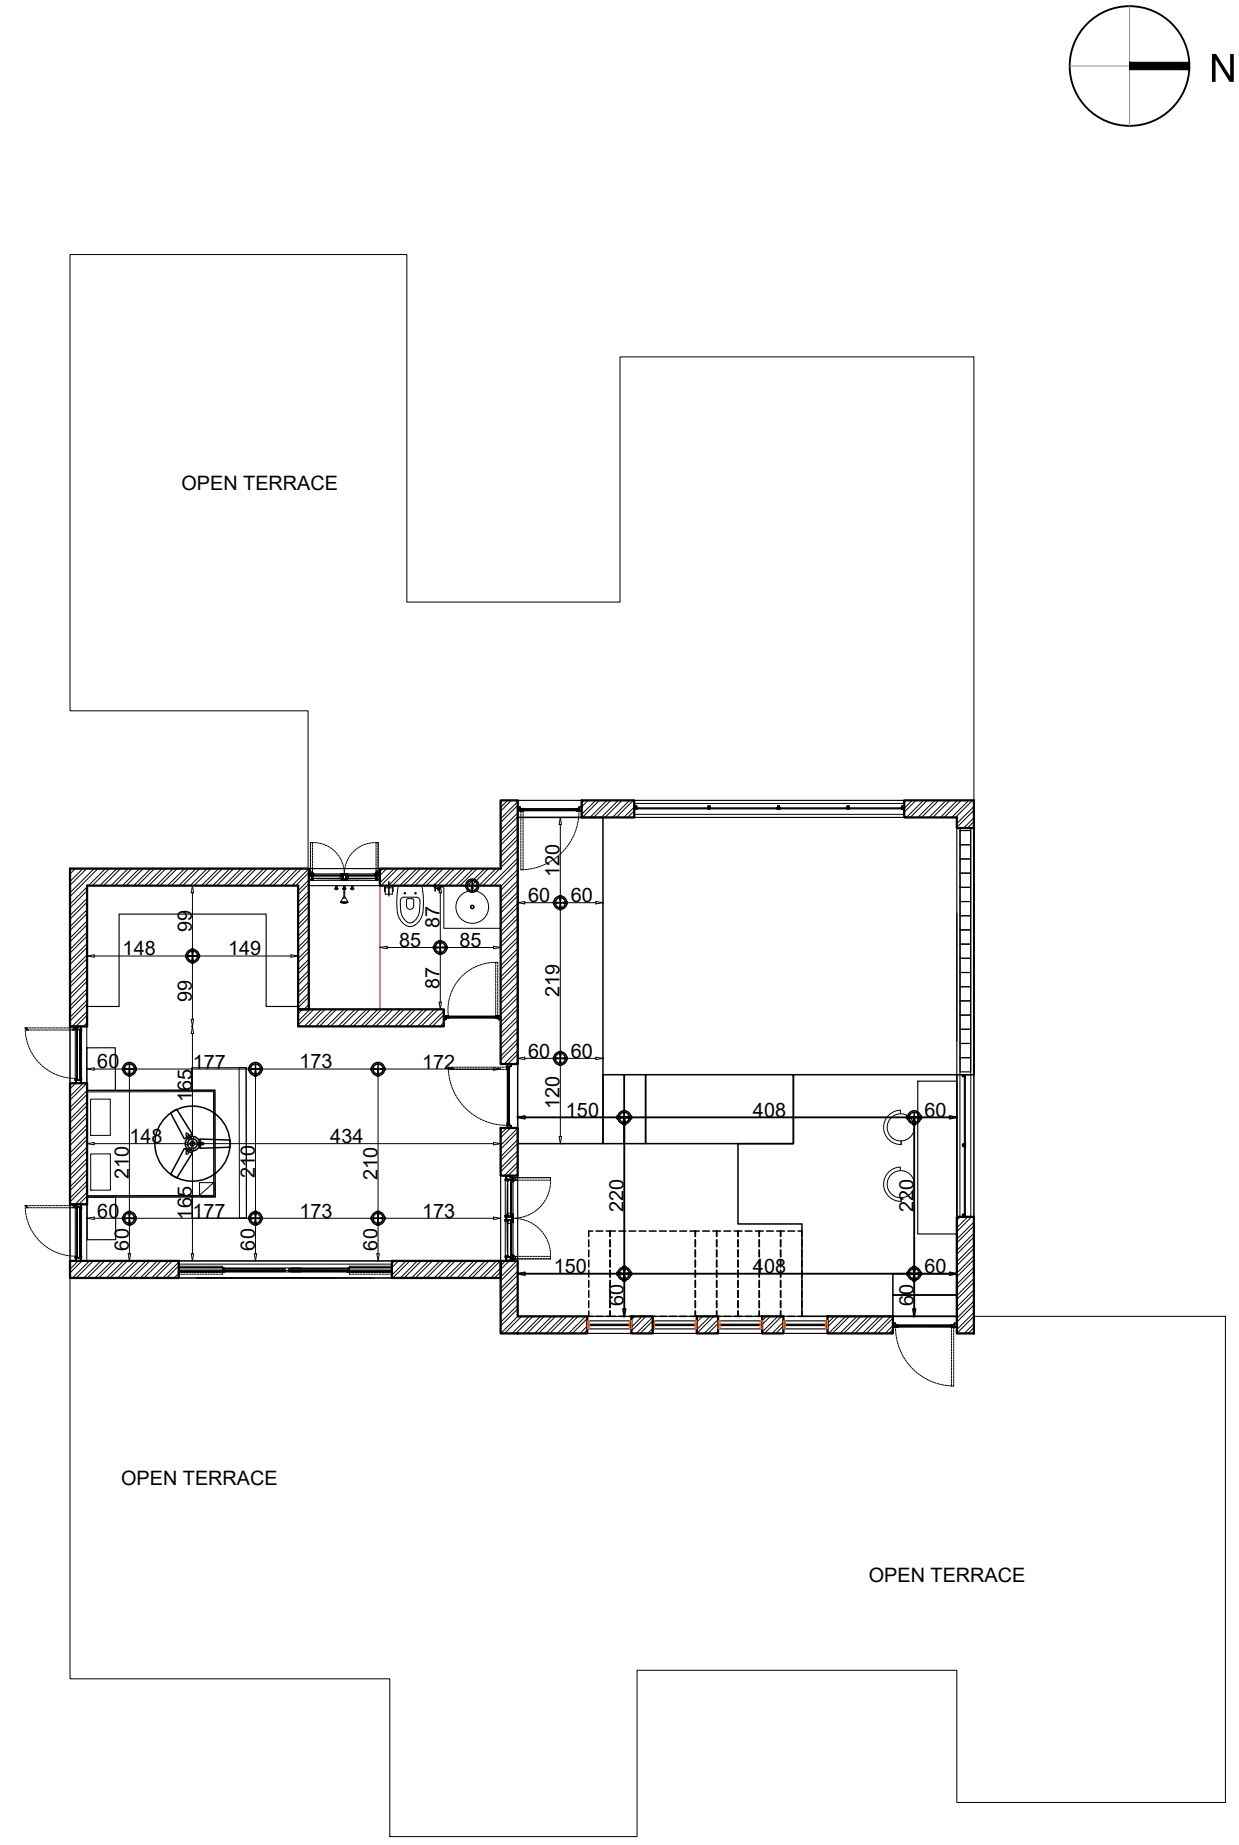

12 **SLAB POINTS**
FIRST FLOOR
SCALE 1:100

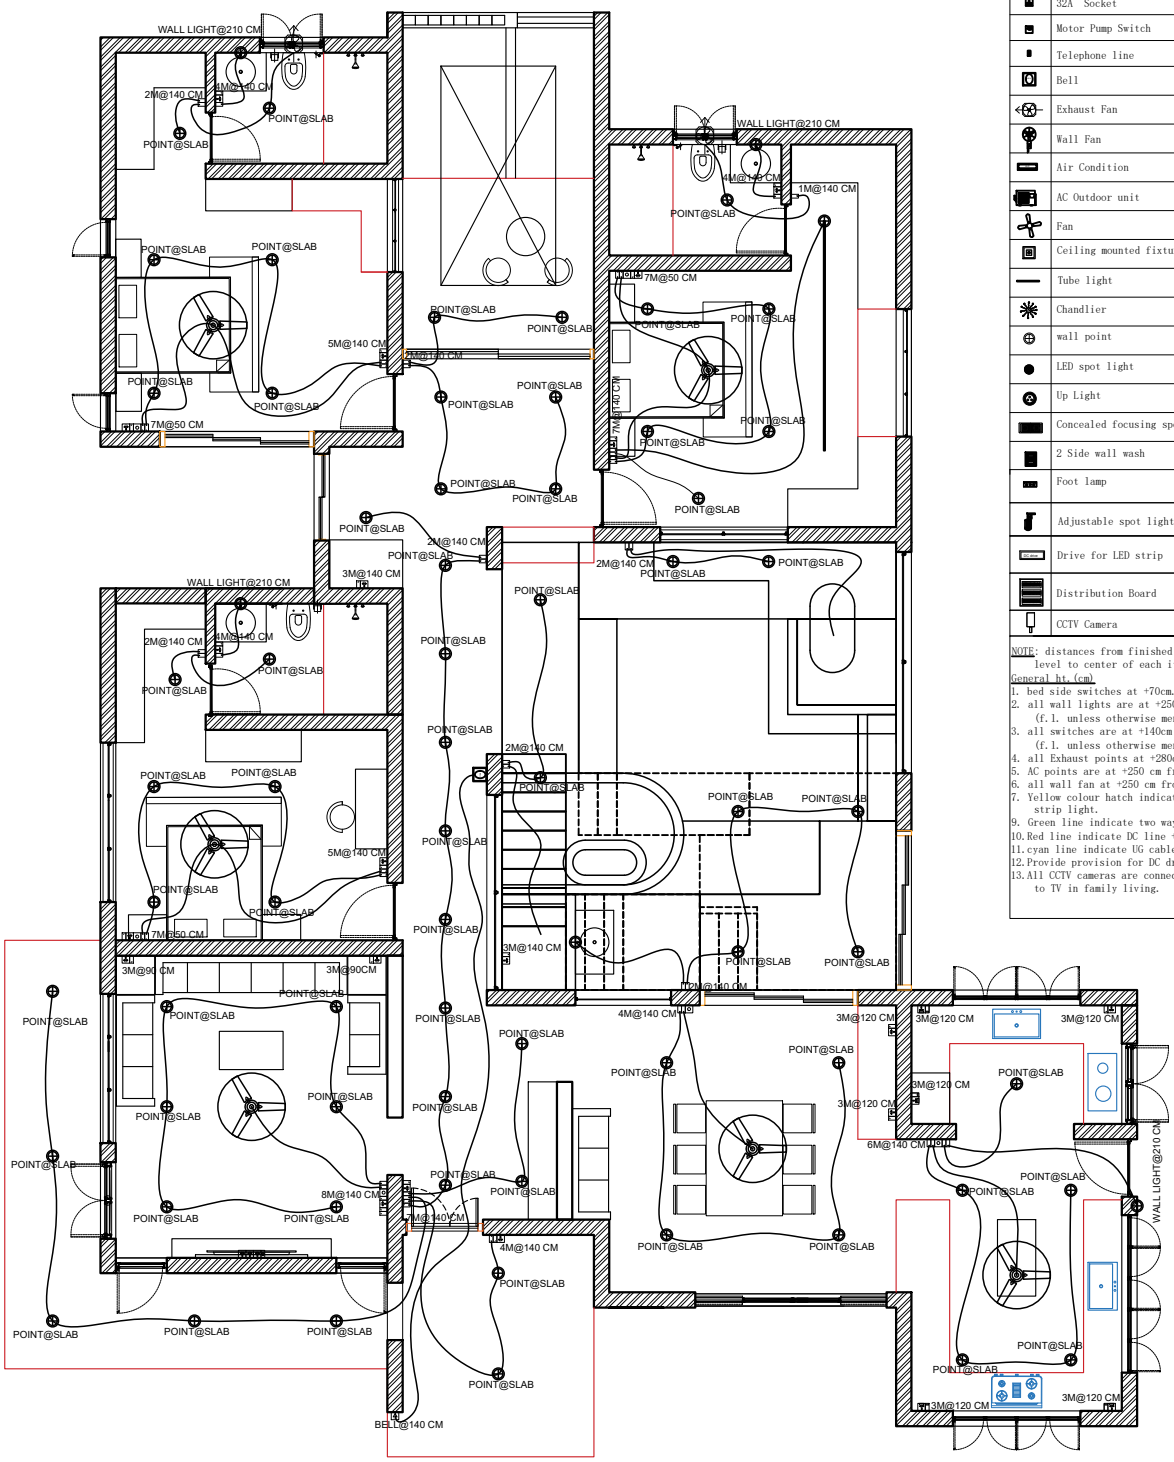

LEGEND

Symbol	Description
	6A Control Switch
	Two way 6A Switch
	6A control Switch
	16A Control Switch
	32A Control Switch
	Master Switch
	Calling Bell Switch
	Fan Regulator
	Cable point
	6A Socket
	16A Socket
	32A Socket
	Motor Pump Switch
	Telephone line
	Bell
	Exhaust Fan
	Wall Fan
	Air Condition
	AC Outdoor unit
	Fan
	Ceiling mounted fixture
	Tube light
	Chandlier
	wall point
	LED spot light
	Up Light
	Concealed focusing spot
	2 Side wall wash
	Foot lamp
	Adjustable spot light
	Drive for LED strip
	Distribution Board
	CCTV Camera


NOTE: distances from finished floor level to center of each items.

General ht.(cm)

1. bed side switches at +70cm.
2. all wall lights are at +250cm from (f.l. unless otherwise mentioned)
3. all switches are at +140cm from (f.l. unless otherwise mentioned)
4. all Exhaust points at +280c from fl.
5. AC points are at +250 cm from fl.
6. all wall fan at +250 cm from fl.
7. Yellow colour hatch indicate LED strip light.
9. Green line indicate two way switch
10. Red line indicate DC line +/-
11. cyan line indicate UG cable
12. Provide provision for DC drive
13. All CCTV cameras are connected to TV in family living.

13 ELECTRICAL PLAN GROUND FLOOR

SCALE 1:100

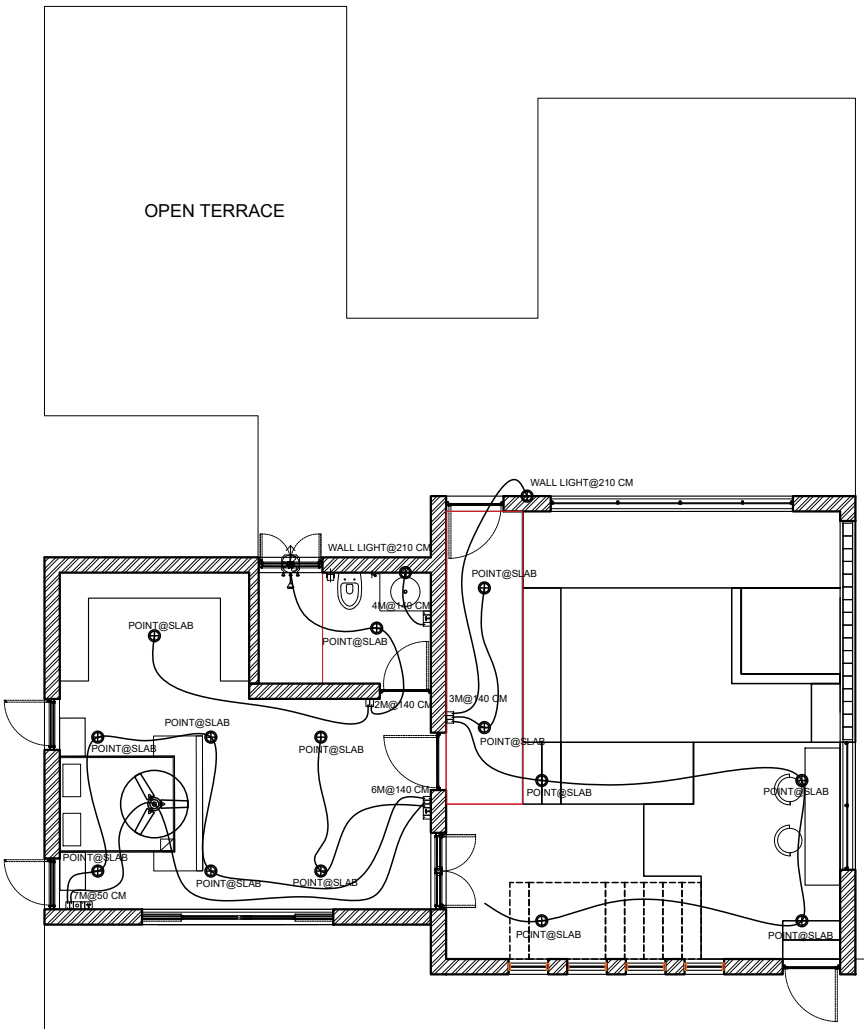

N

LEGEND

Symbol	Description
	6A Control Switch
	Two way 6A Switch
	6A control Switch
	16A Control Switch
	32A Control Switch
	Master Switch
	Calling Bell Switch
	Fan Regulator
	Cable point
	6A Socket
	16A Socket
	32A Socket
	Motor Pump Switch
	Telephone line
	Bell
	Exhaust Fan
	Wall Fan
	Air Condition
	AC Outdoor unit
	Fan
	Ceiling mounted fixture
	Tube light
	Chandlier
	wall point
	LED spot light
	Up Light
	Concealed focusing spot
	2 Side wall wash
	Foot lamp
	Adjustable spot light
	Drive for LED strip
	Distribution Board
	CCTV Camera

NOTE: distances from finished floor level to center of each items.

General ht.(cm)

1. bed side switches at +70cm.
2. all wall lights are at +250cm from (f.l. unless otherwise mentioned)
3. all switches are at +140cm from (f.l. unless otherwise mentioned)
4. all Exhaust points at +280c from fl.
5. AC points are at +250 cm from fl.
6. all wall fan at +250 cm from fl.
7. Yellow colour hatch indicate LED strip light.
9. Green line indicate two way switch
10. Red line indicate DC line +/-
11. cyan line indicate UG cable
12. Provide provision for DC drive
13. All CCTV cameras are connected to TV in family living.

13 ELECTRICAL PLAN
FIRST FLOOR
SCALE 1:100